





## PERSONAL DETAILS

NAME ; SARATH KUMAR S  
SEX ; MALE  
DOB ; 30JUNE 1994  
NATIONALITY ; INDIAN

ADDRESS :  
“SARATH BHARVAN”  
Methamcode ,vandazhy(PO)  
Palakkad (dist;)  
PIN ; 678 706  
PH ; 04922-261273

## CONTACT

sarathvandazhy@gmail.com

+91-9809520720

## PHOTOGRAPHY



## PAINTING



## GAMING



## - HOBBY -

## TRAVELLING



## OBSERVING



## BROWSING



## PERSONAL LANDMARKS

CONDUCTED ZONASA 2012  
ATTENDED ZONASA 2015  
PARTICIPATED IN ANDC  
DESIGN PROJECT  
MEMBER OF SSA @ SCOA

## FIELD OF INTEREST

INTERIOR DESIGN  
PRODUCT DESIGN  
MODEL MAKING  
LANDSCAPING

## REFERENCE

SNEHA COLLEGE OF ARCHITECTURE  
ATTRAYAMPATHY,KOLLENGODE  
PALAKKAD (DIST)  
snehacollegeofarchitecture@gmail.com

## SOFTWARE SKILLS

AUTO CAD  
SKETCH UP  
PHOTOSHOP  
REVIT ARCHITECTURE  
RHINO  
3D MAX  
V-RAY  
SU-PODIUM  
MOVIE MAKER  
MICROSOFT OFFICE  
ADOBE AUDITION  
“ ACROBAT  
“ AFTER EFFECTS  
“ LIGHT ROOM  
“ INDESIGN  
“ ILLUSTRATOR

## DESIGN PROJECTS


S1 & S2 - BASIC DESIGN  
S3 - RESIDENCE & CAFETERIA  
S4 - PRIMARY SCHOOL &  
ROW HOUSING  
S5 - BUS STATION & OFFICE

## MANUAL SKILLS




MODELING SKETCHING PAINTING



semester 1 & 2

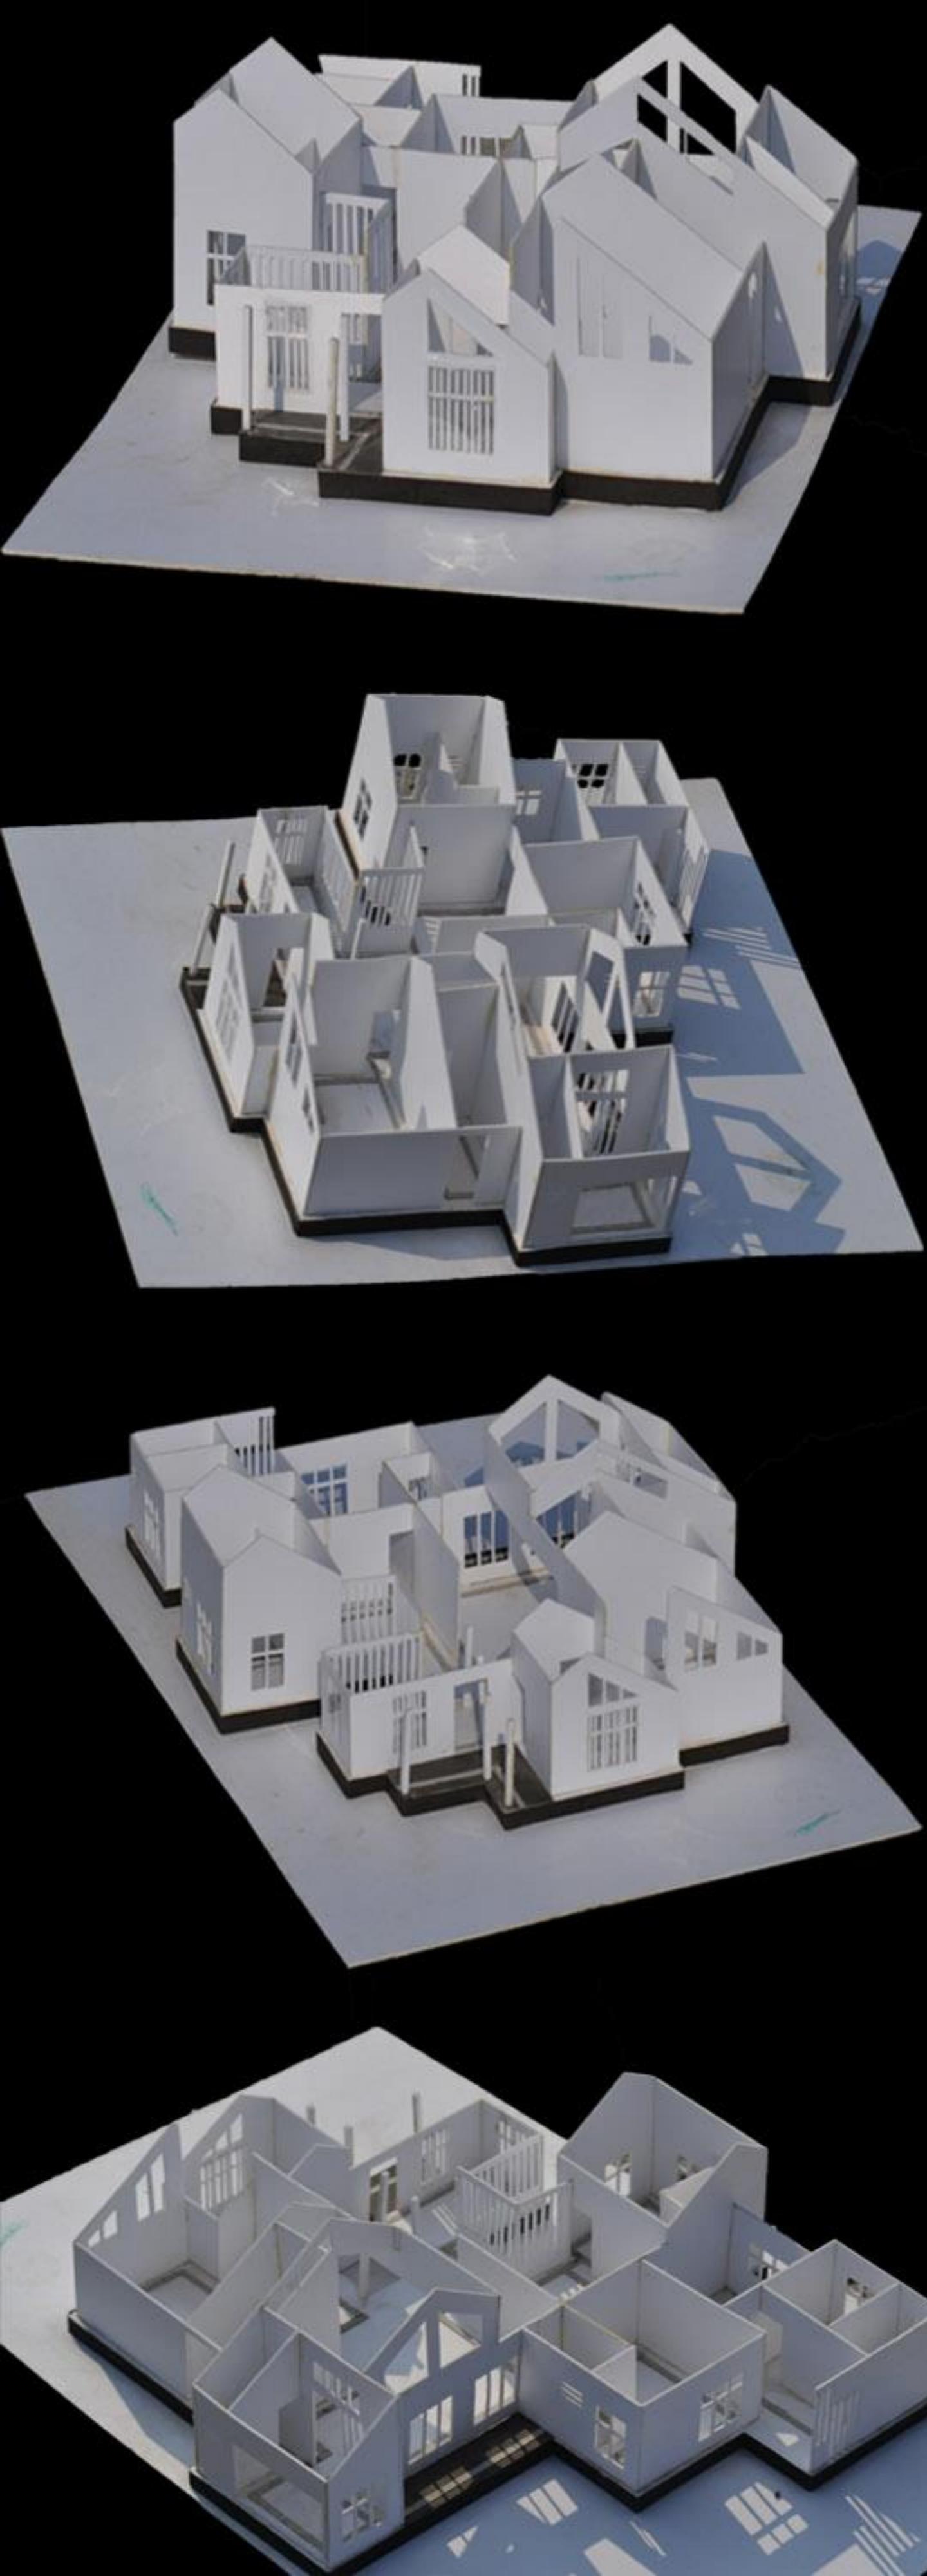

# INTER LOCKING SPACES

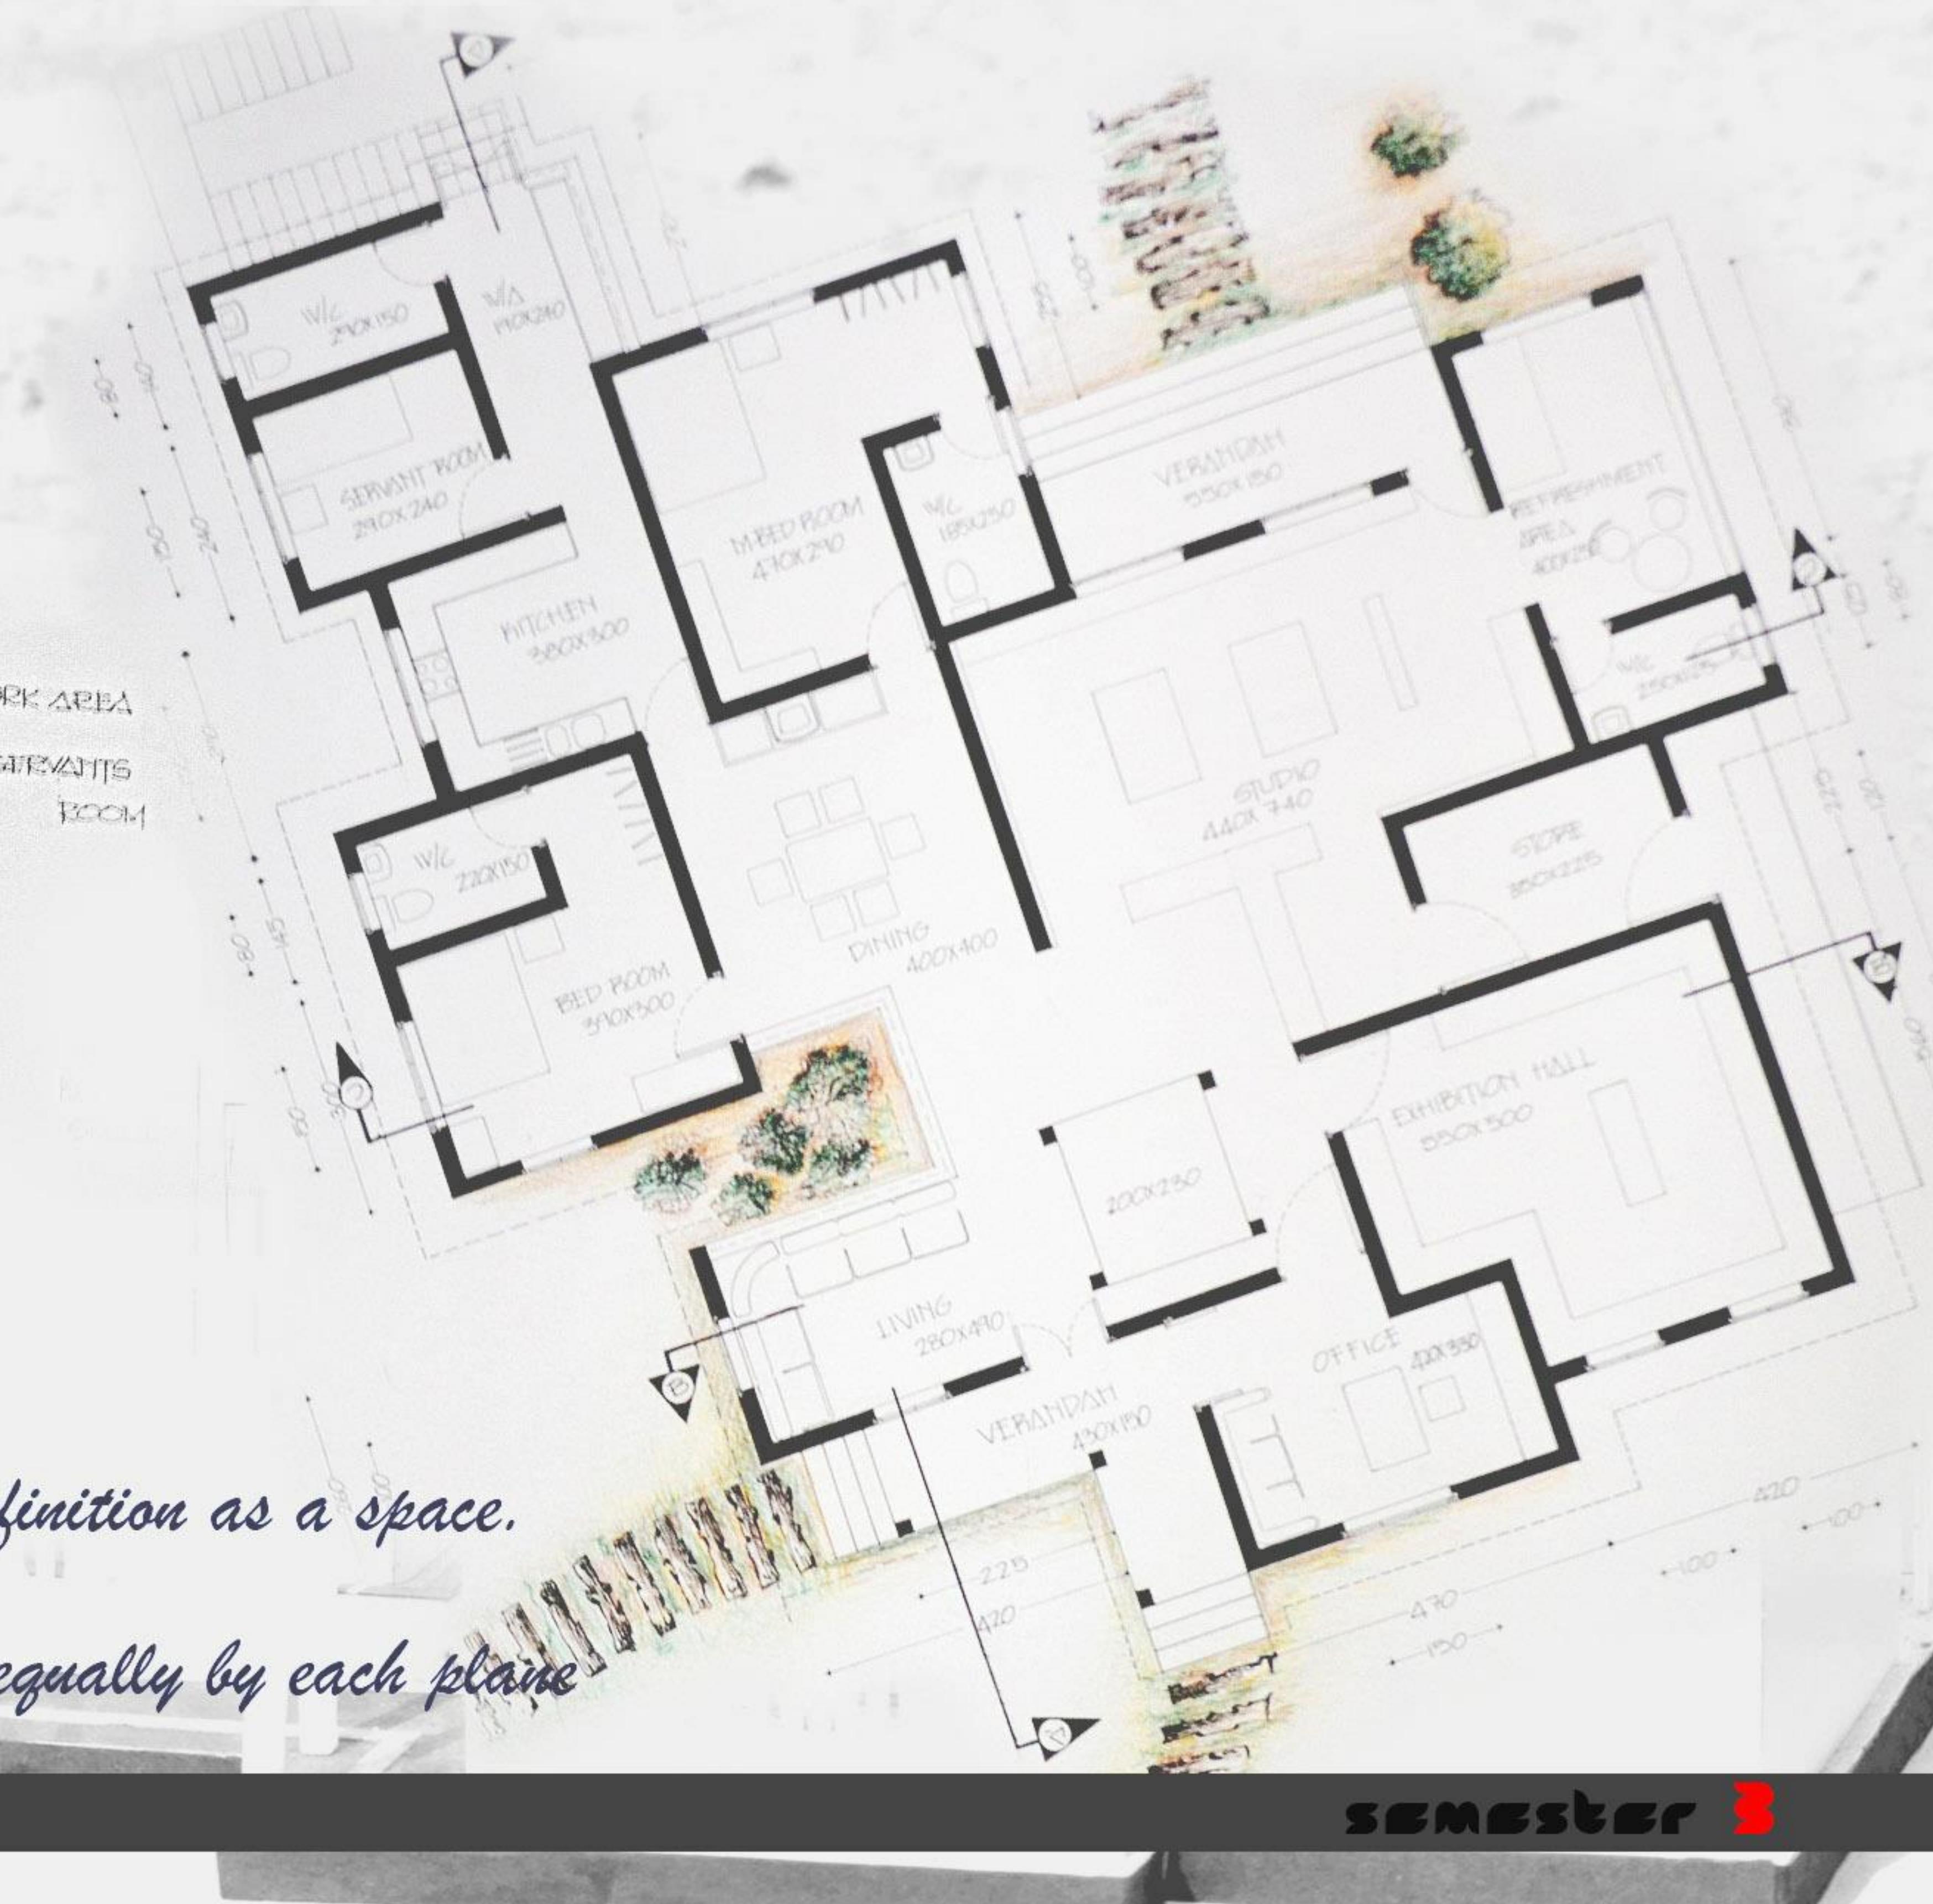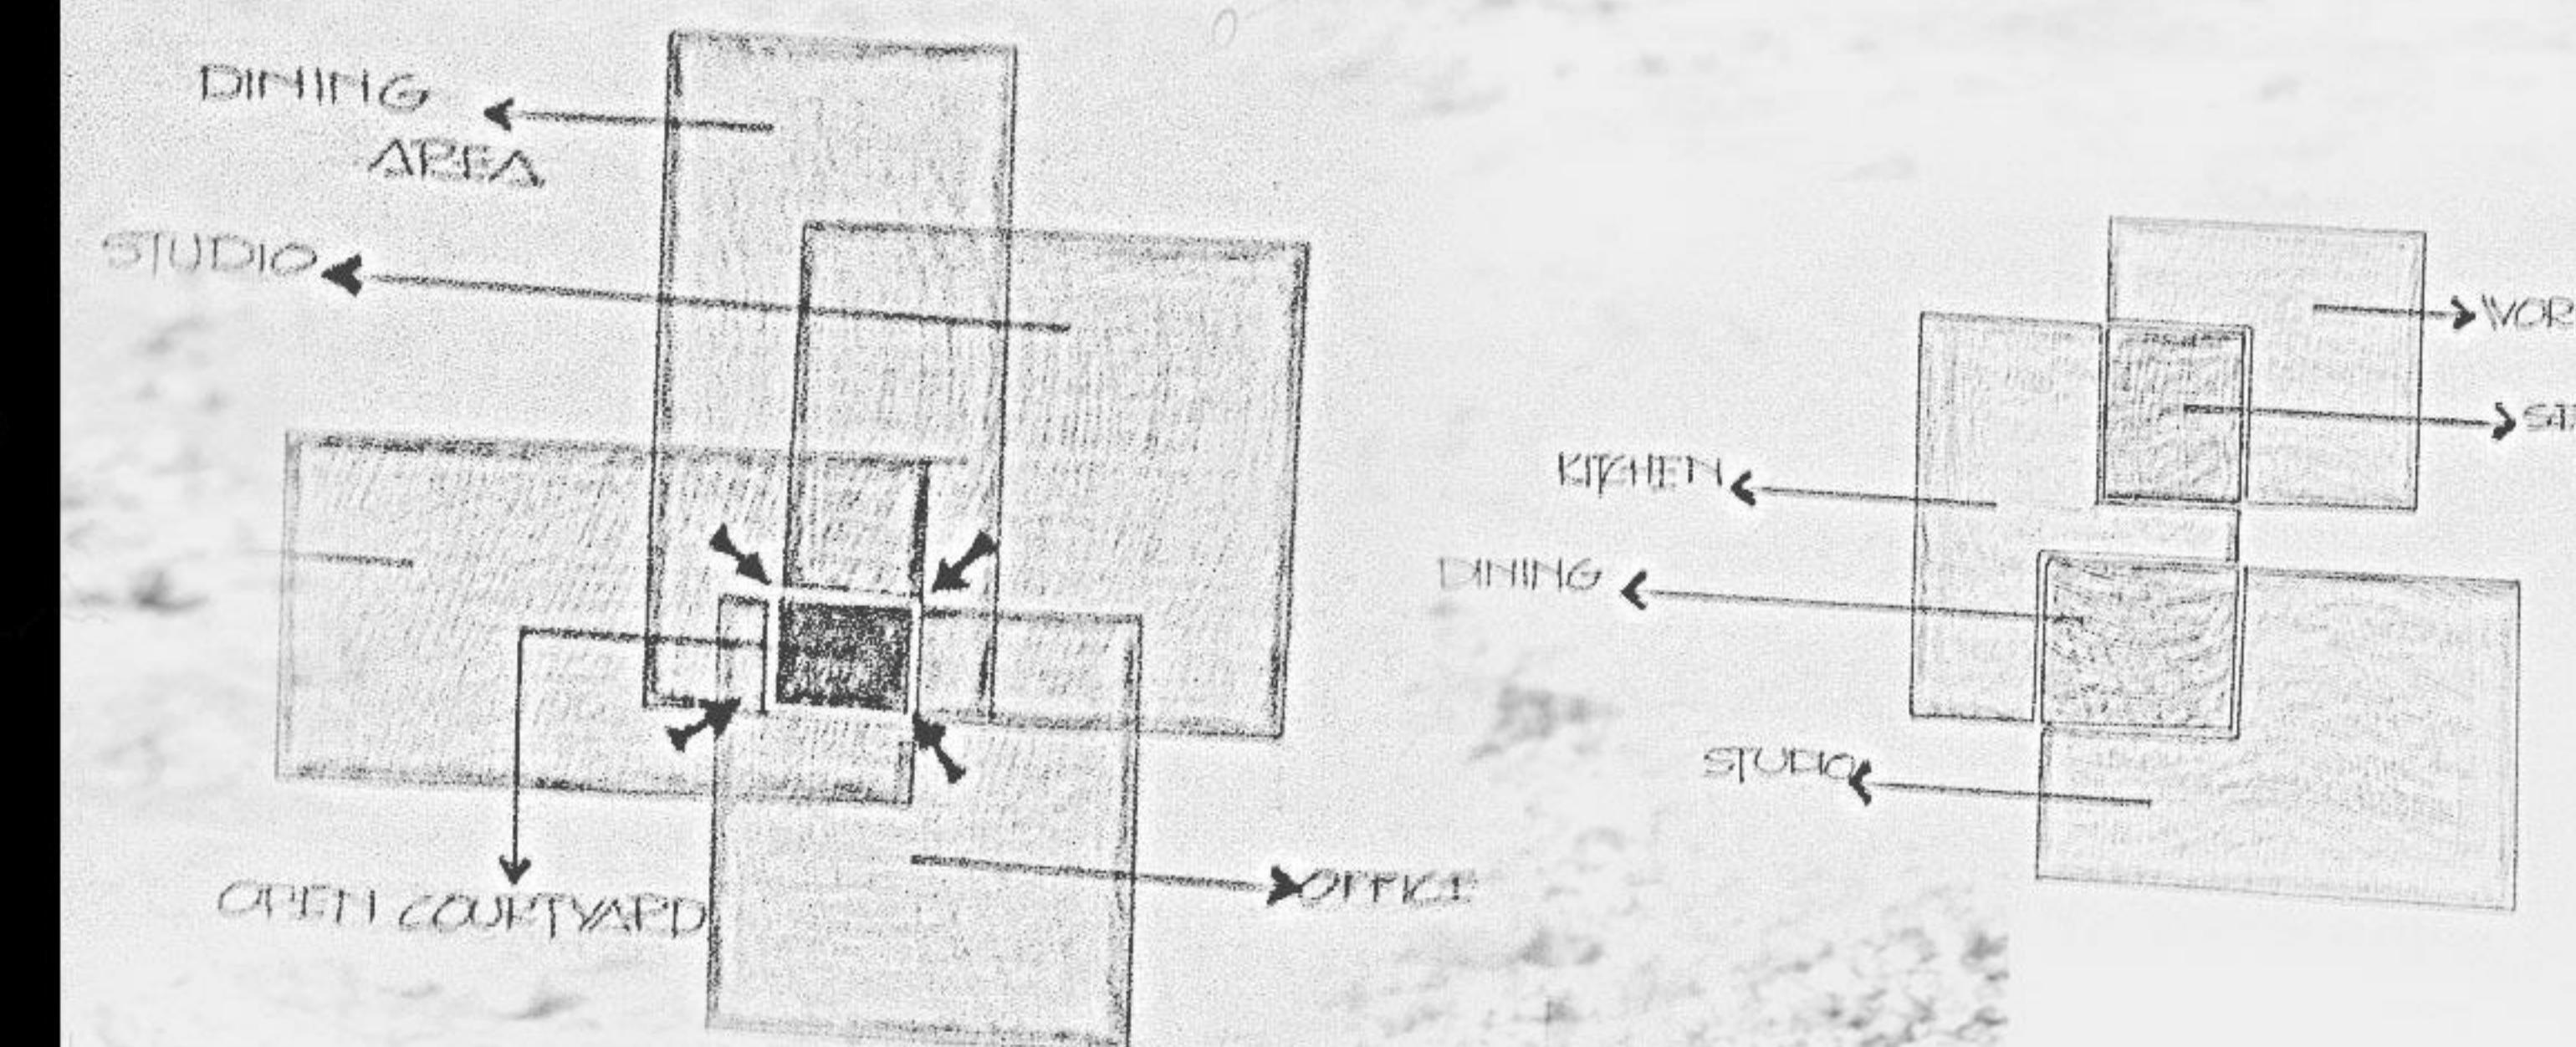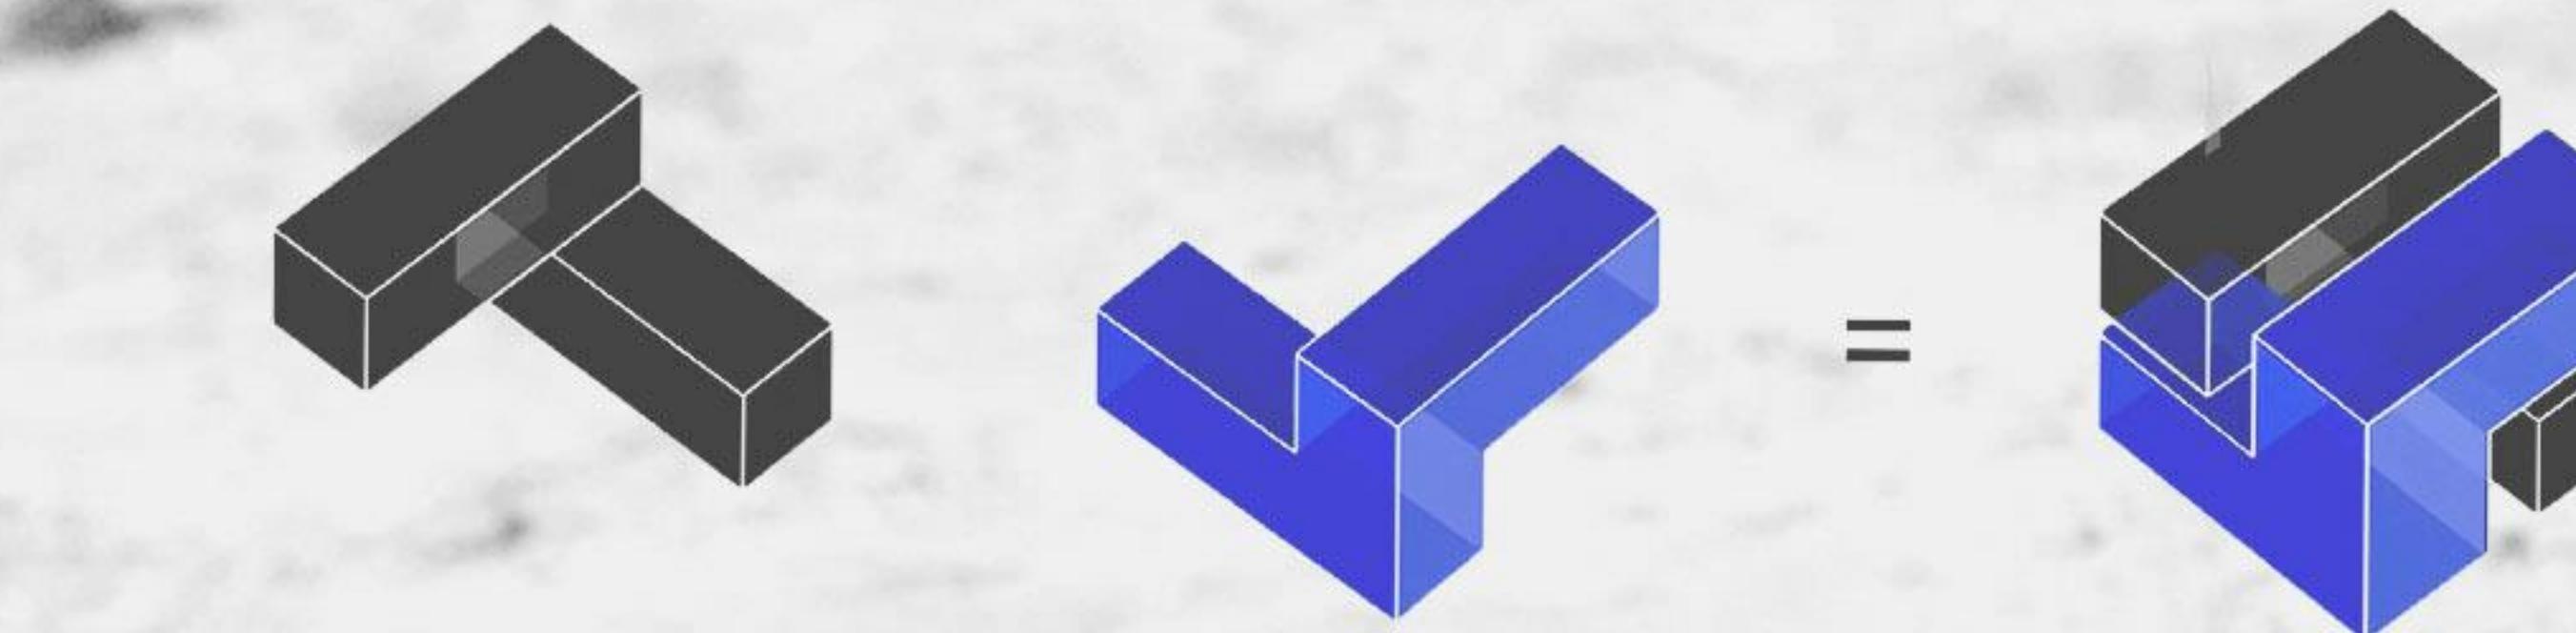


Residence


The spatial fields overlap the volume of another space.

When two spaces interlock each retains its identity and definition as a space.

The interlocking portion of the two volumes can be shared equally by each plane

# cafeteria

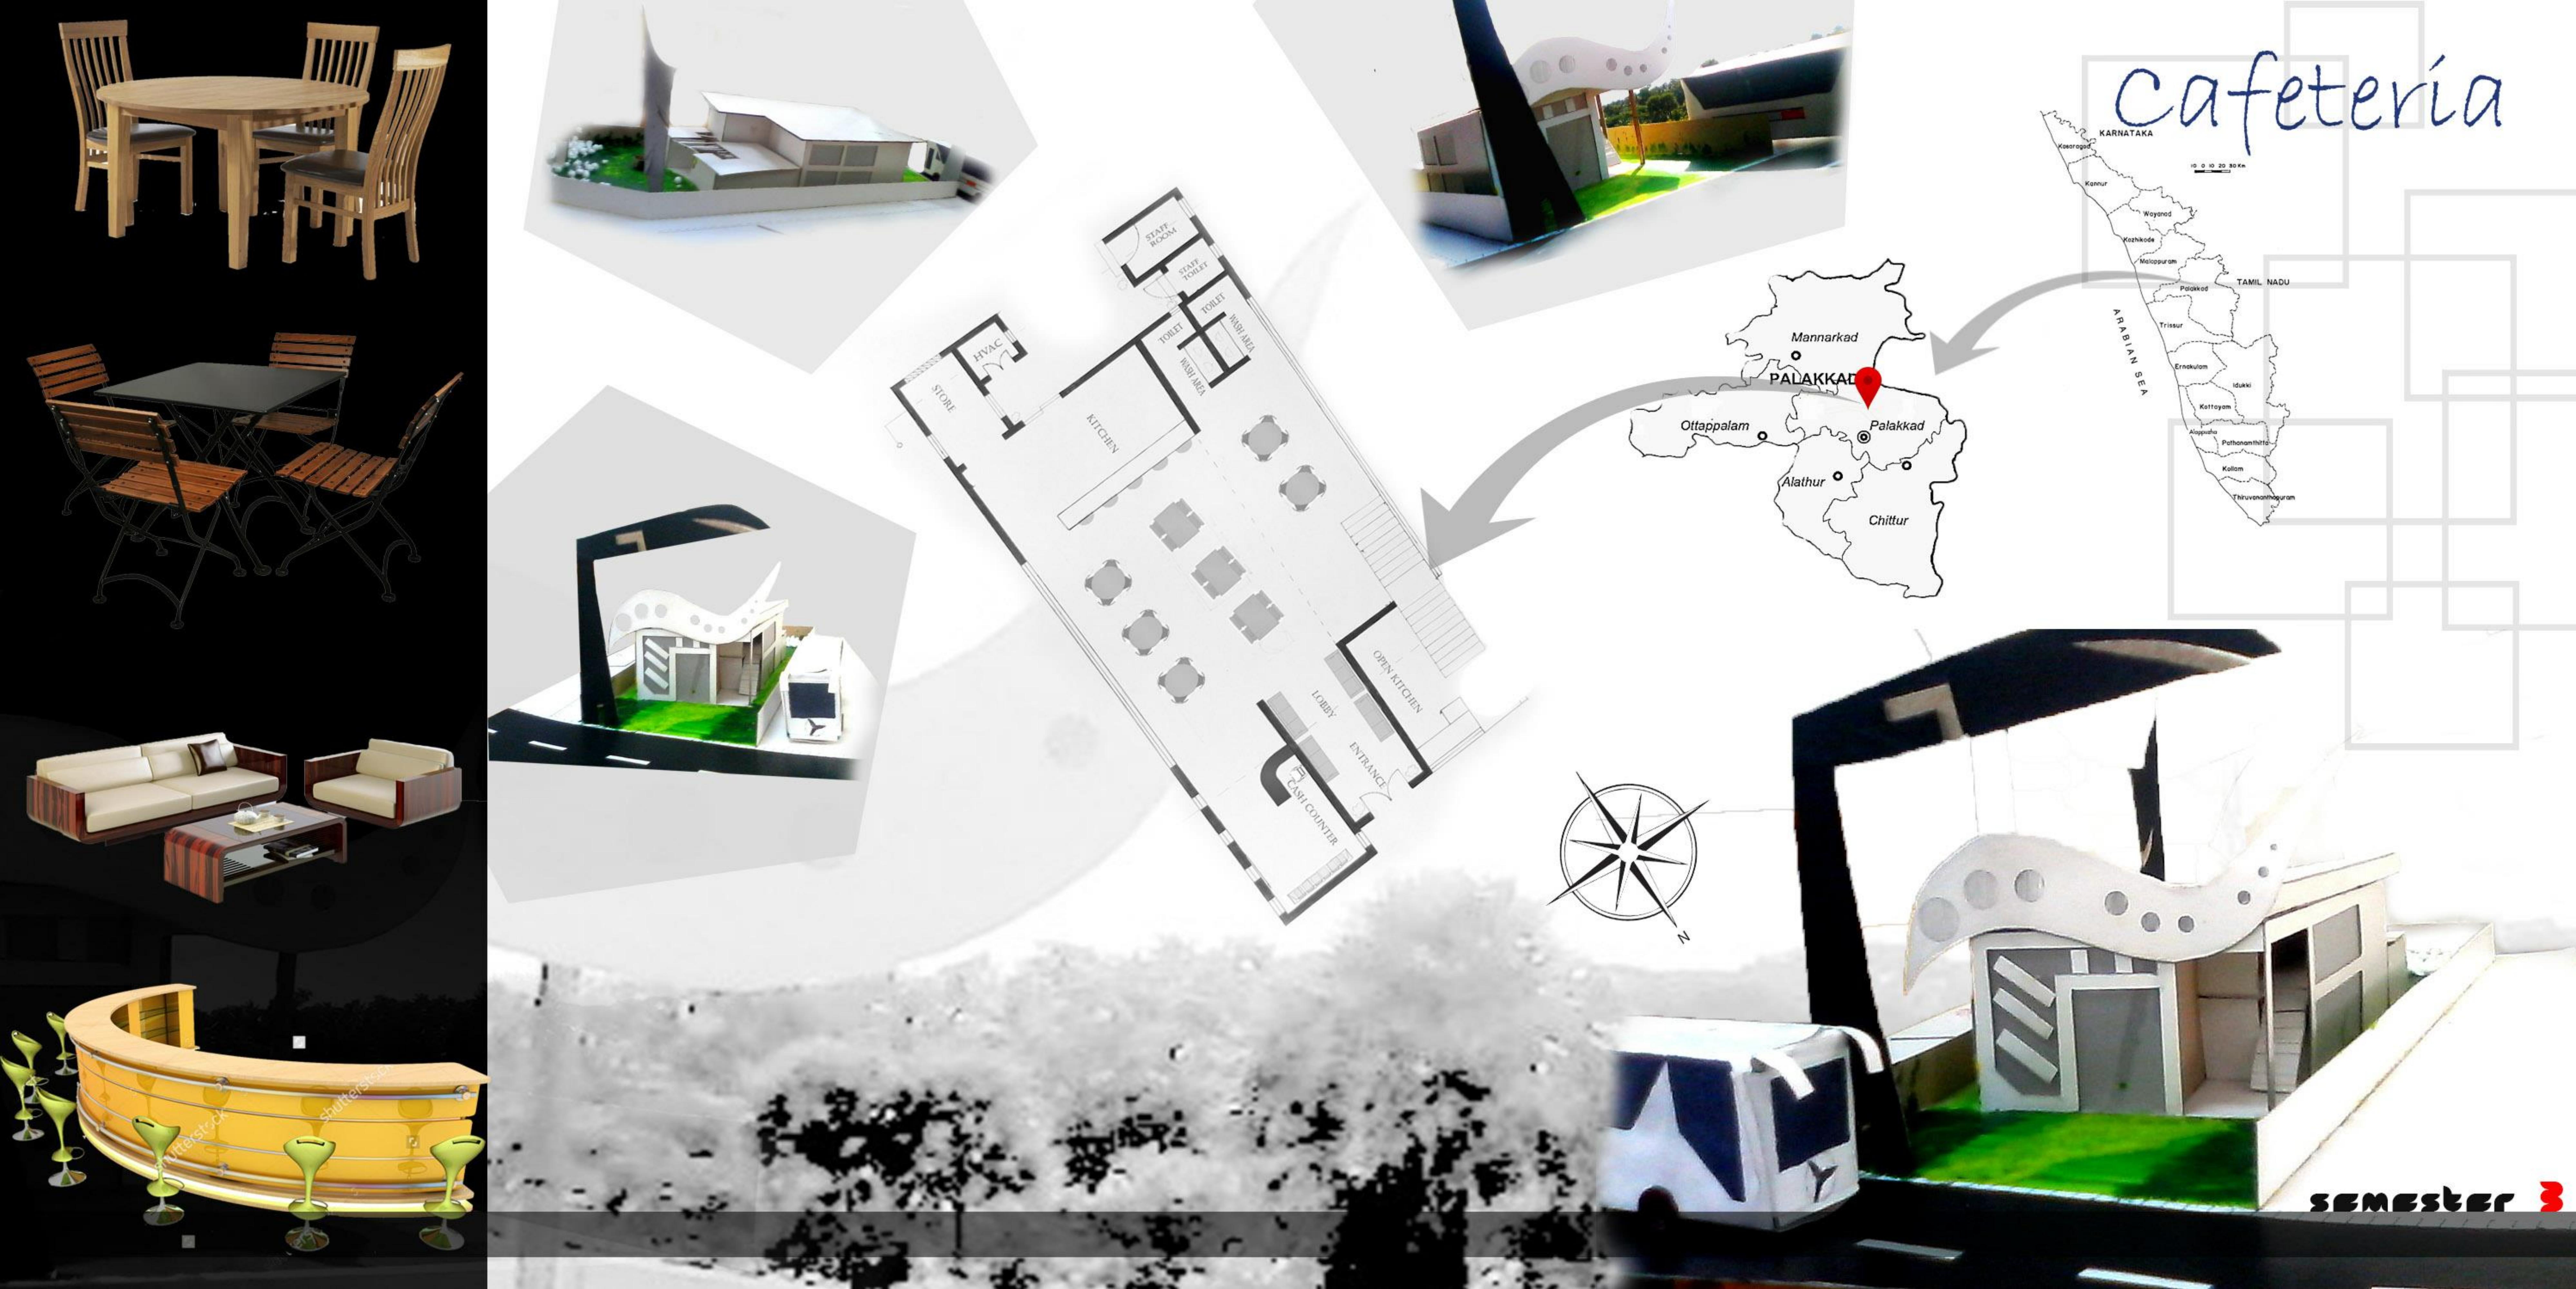


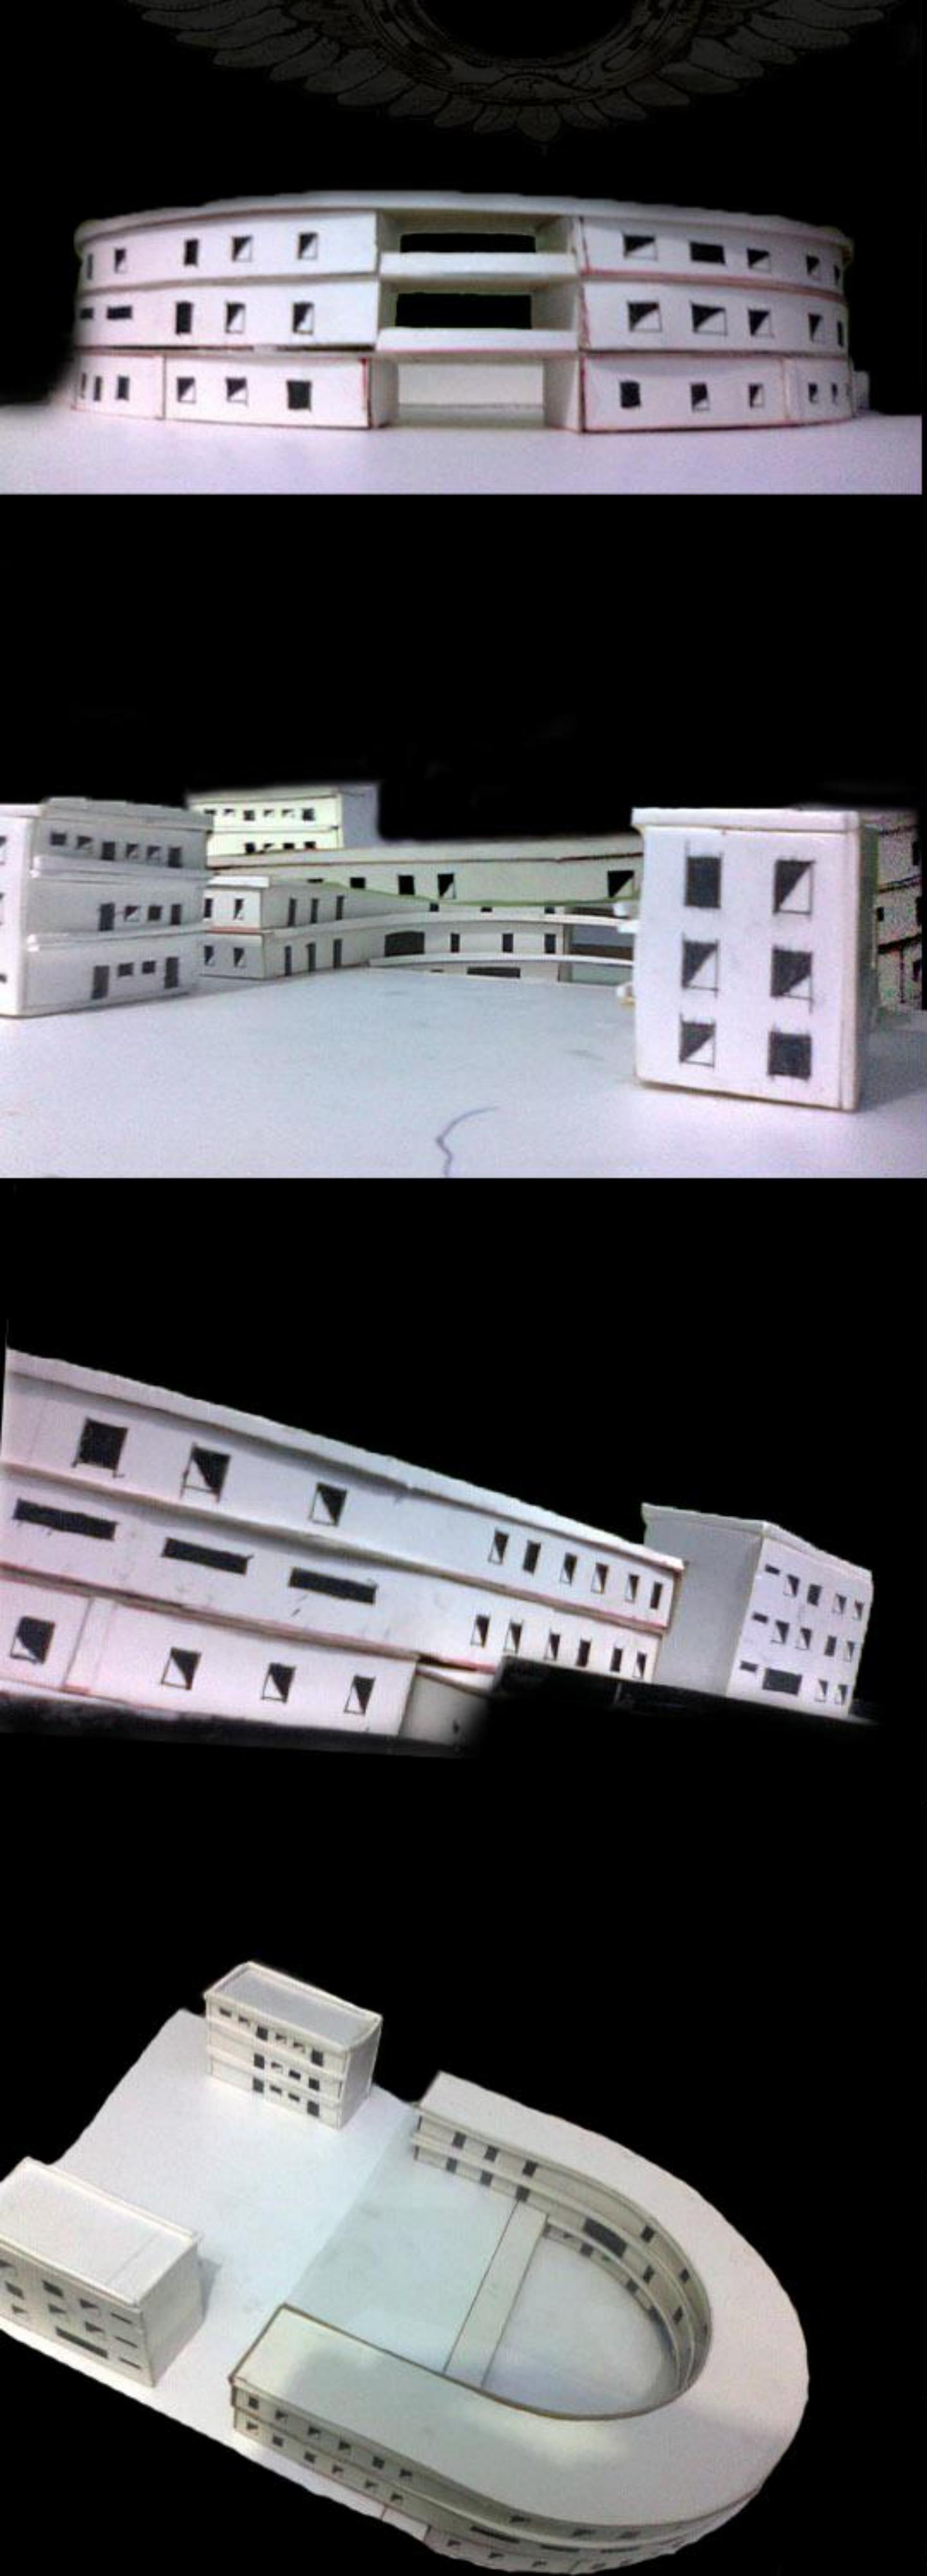

# Concept - Horse shoe

a horseshoe is said to bring good luck.

Some believe that to hang it with the ends pointing upwards is good luck


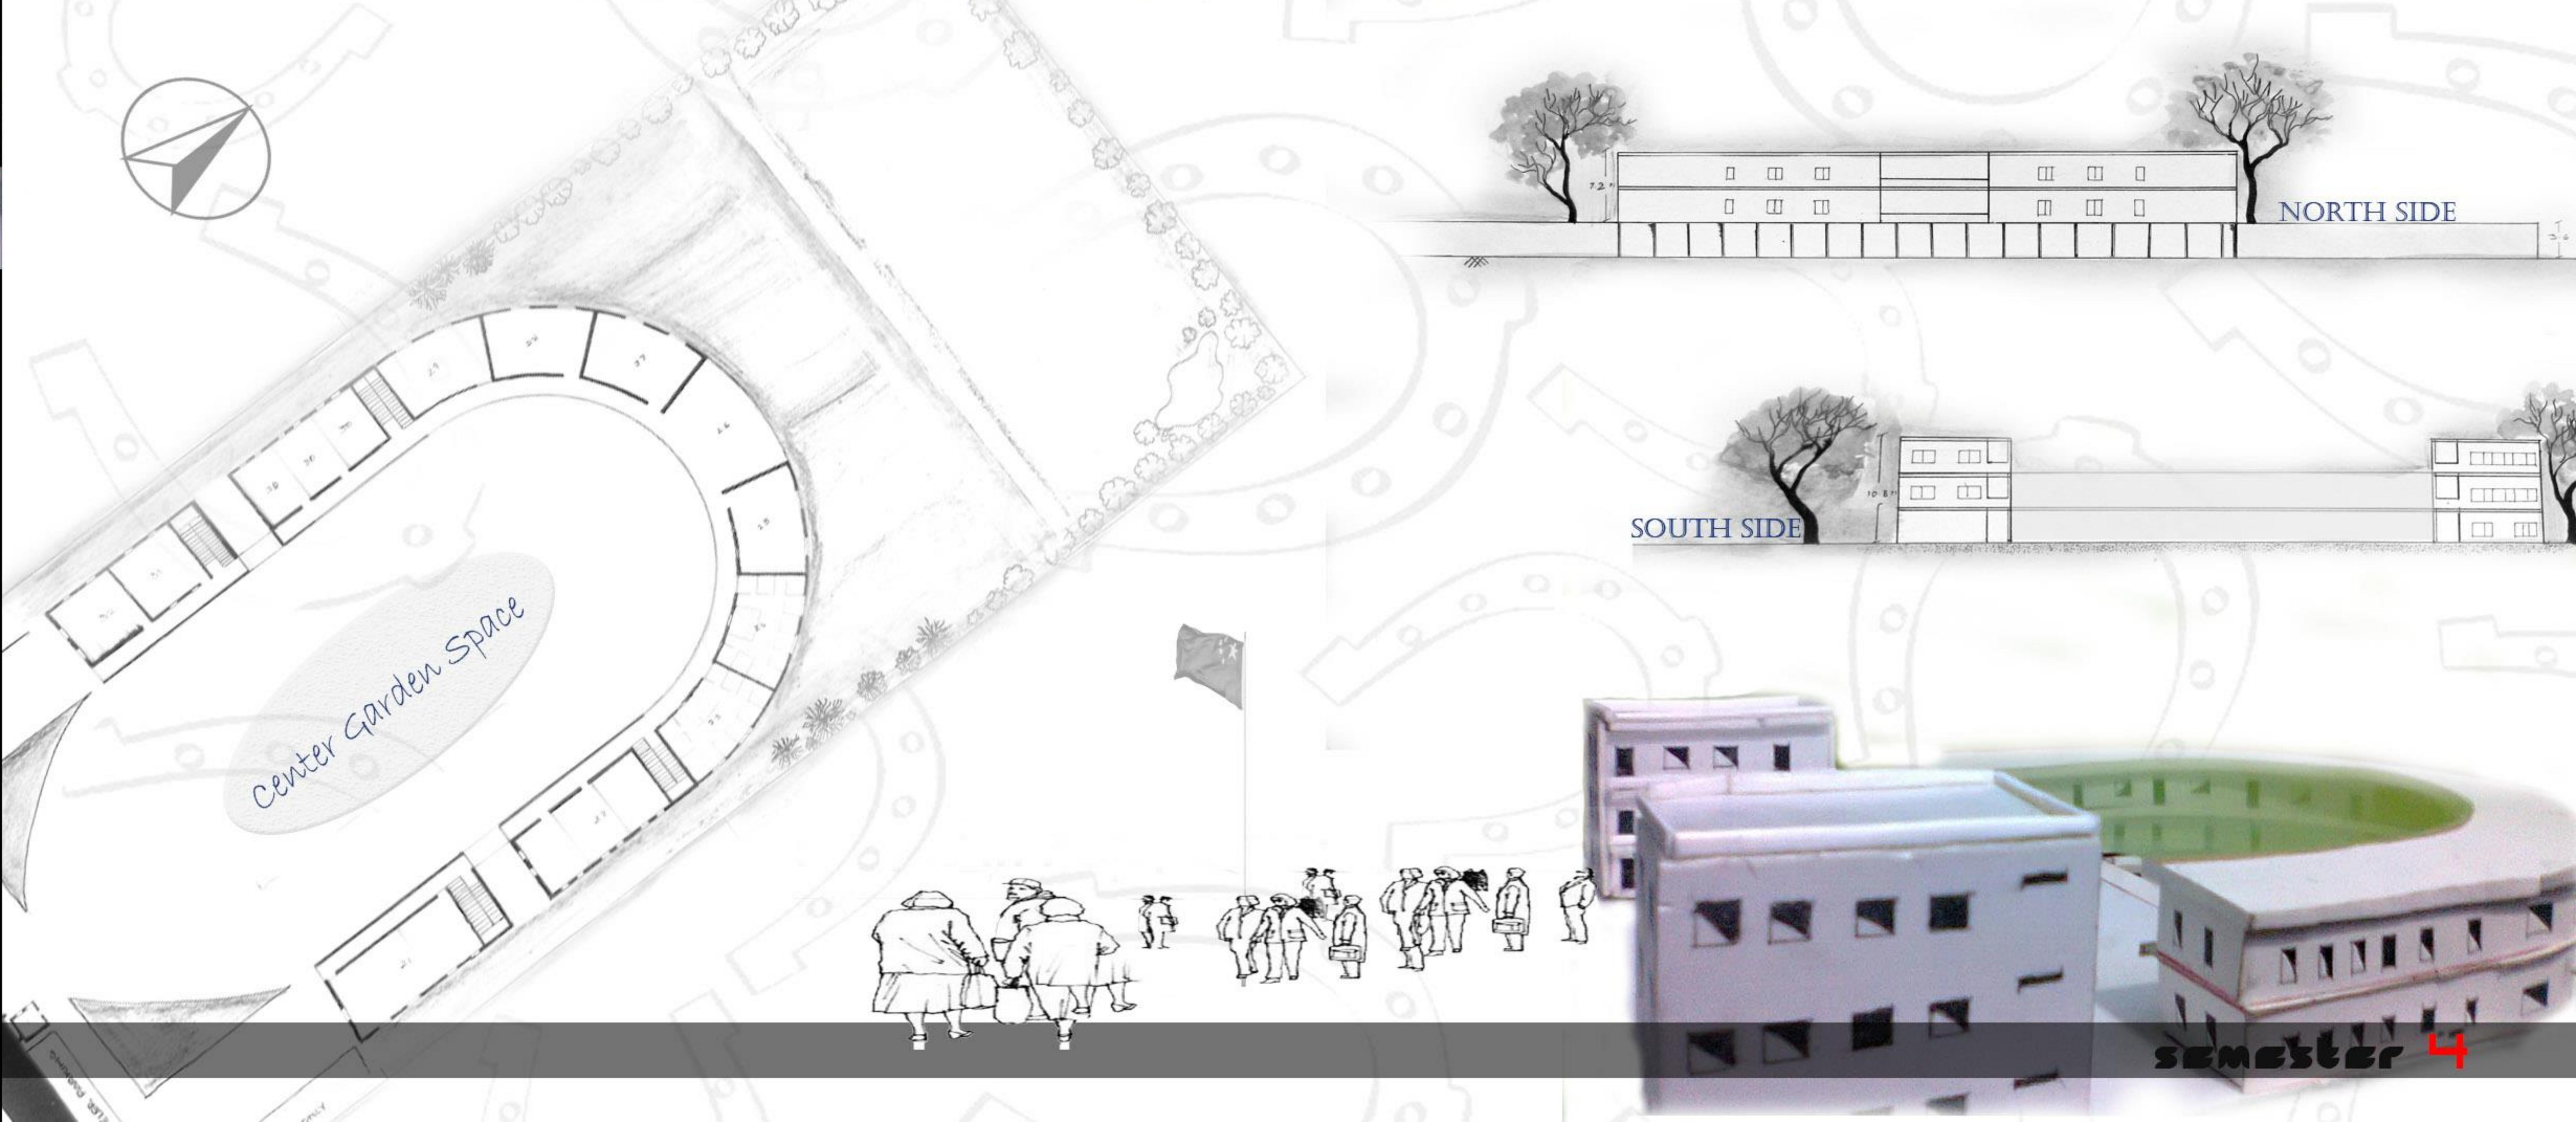


# OFFICE COMPLEX & BUS STATION











- 1:Office Space
- 2:Cabin Space
- 3:Lift
- 4>Toilets
- 5:Staircase
- 6: Manager Cabin
- 7: Asst. Manger
- 8: Security
- 9:Dining
- 10: Common Toilets
- 11:Wash Area
- 12:Store
- 13: Vegetation
- 14:Two wheeler parking
- 15:Bus station
- 16:Waiting Area
- 17:Shops
- 18:Bus Bays
- 19: Entry
- 20:Exit

AREA - 26061.95 SQ.METER

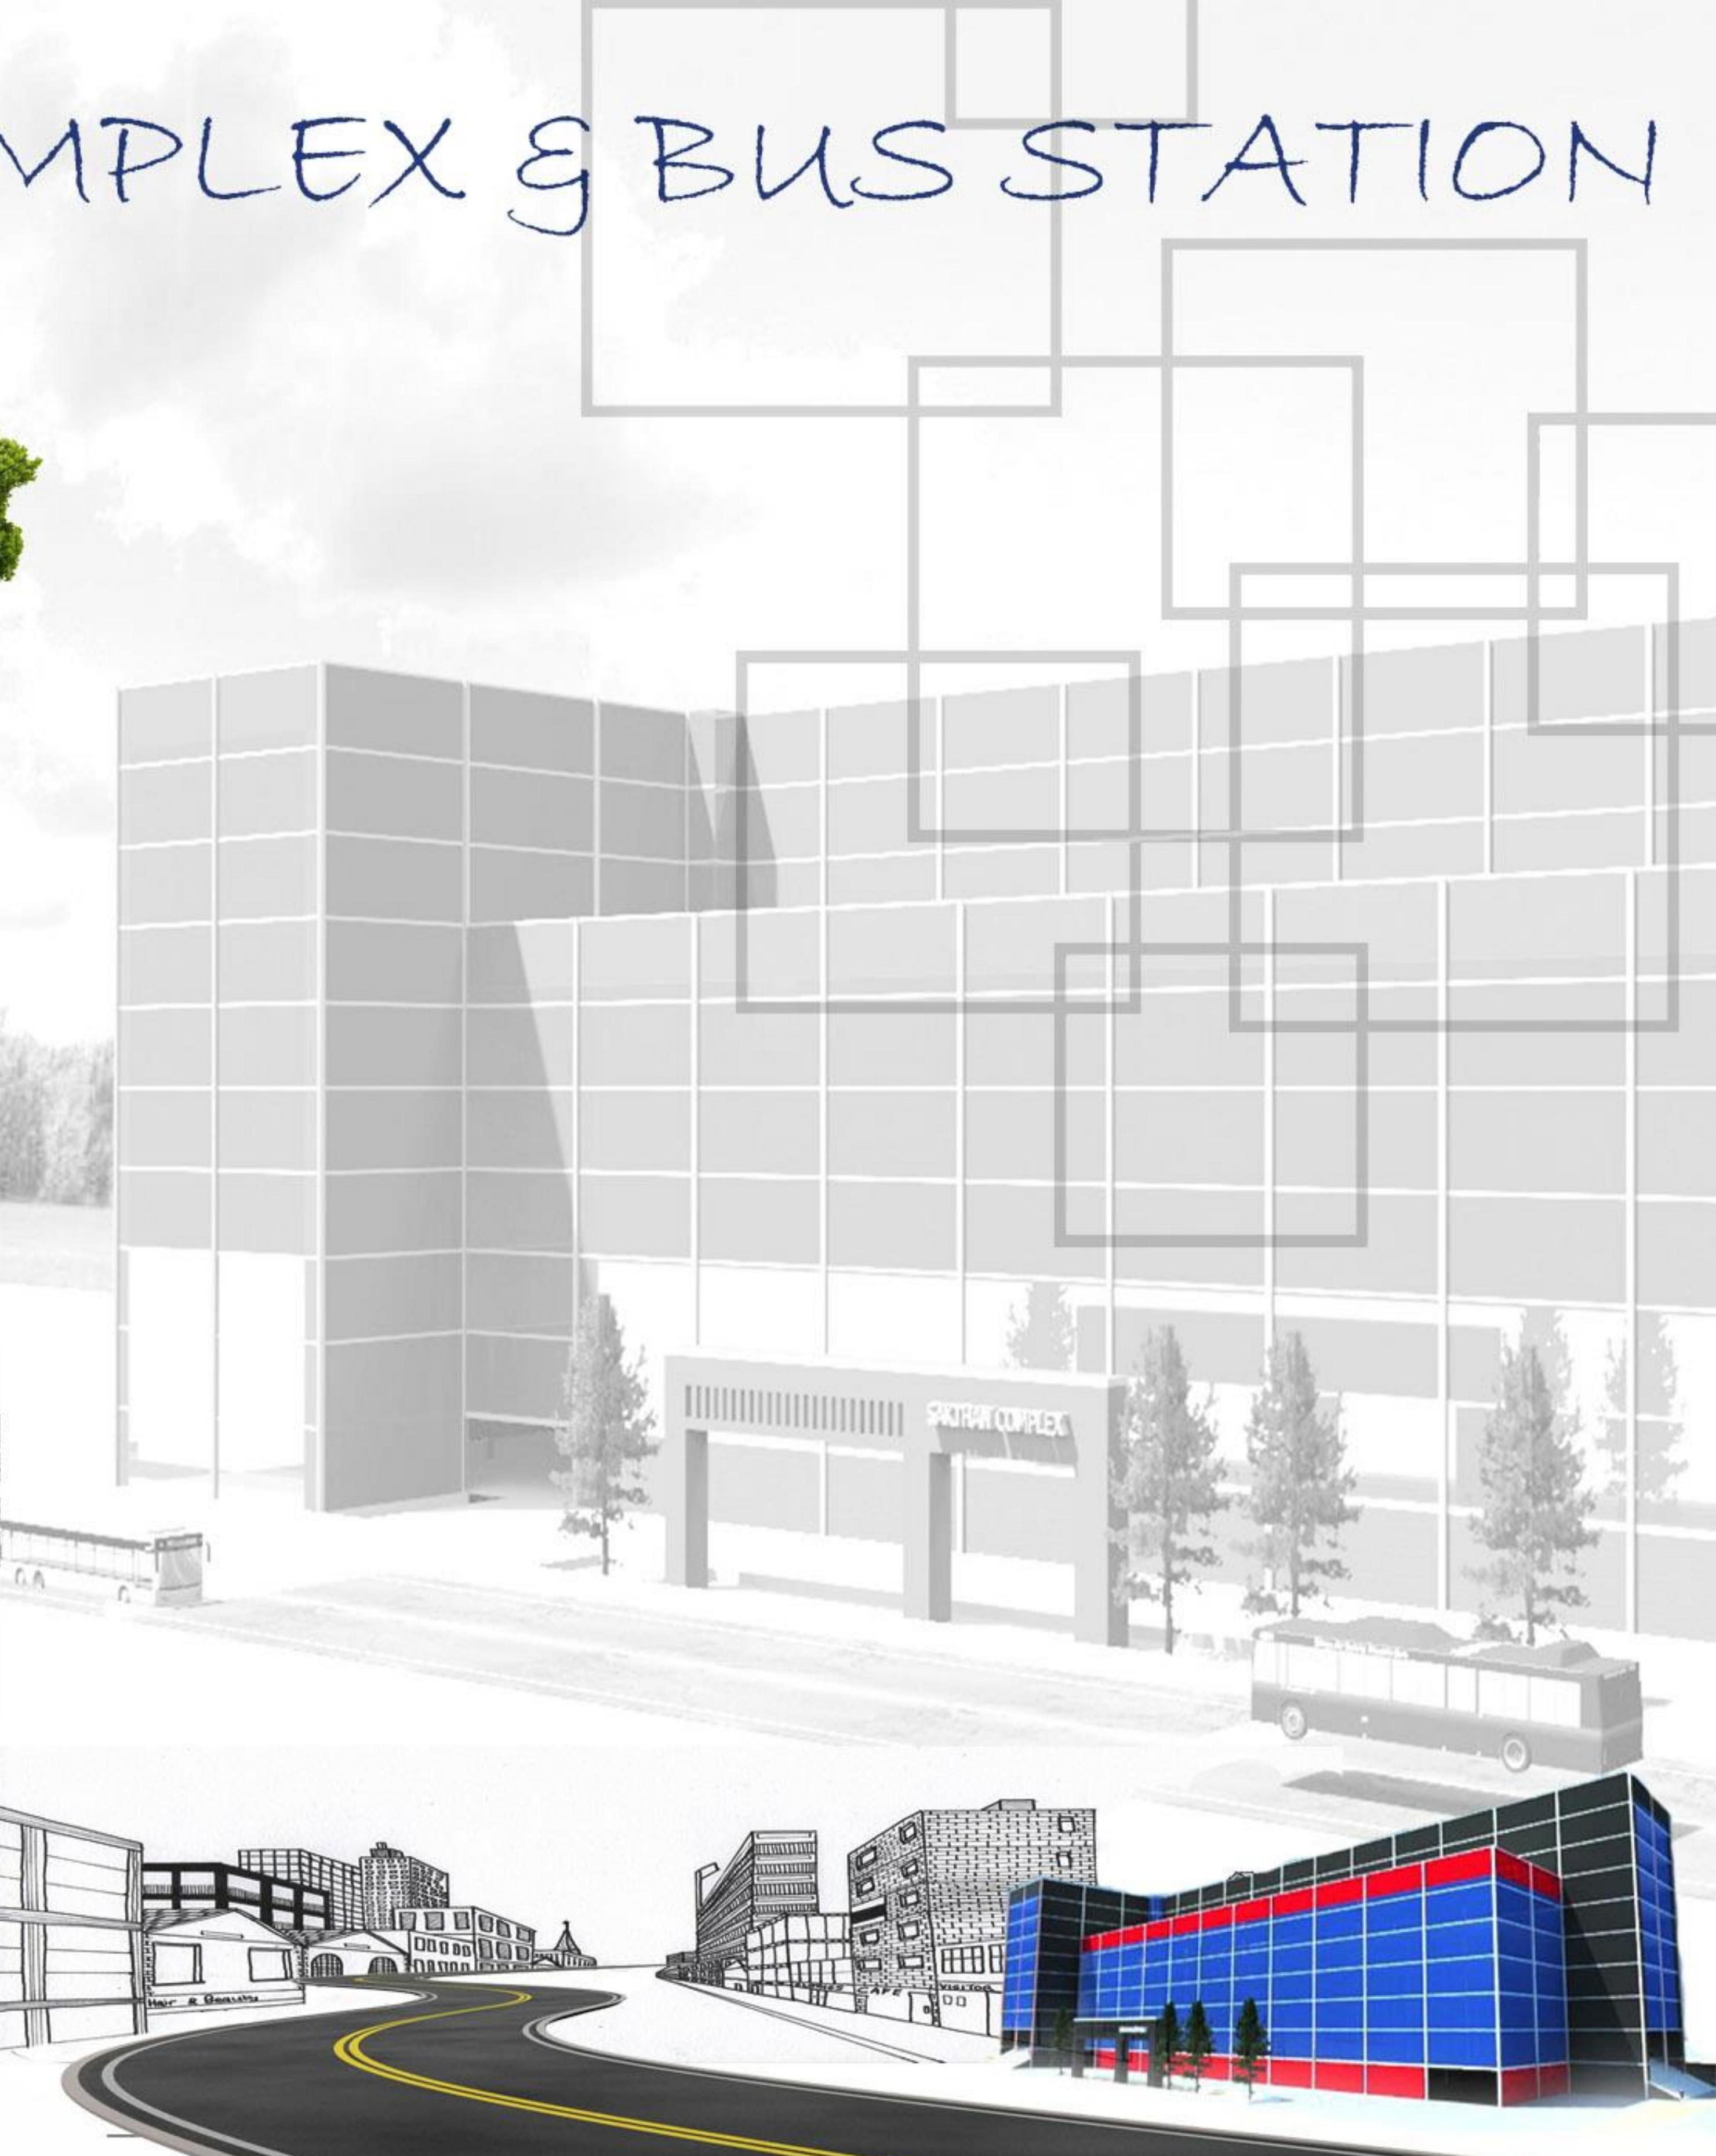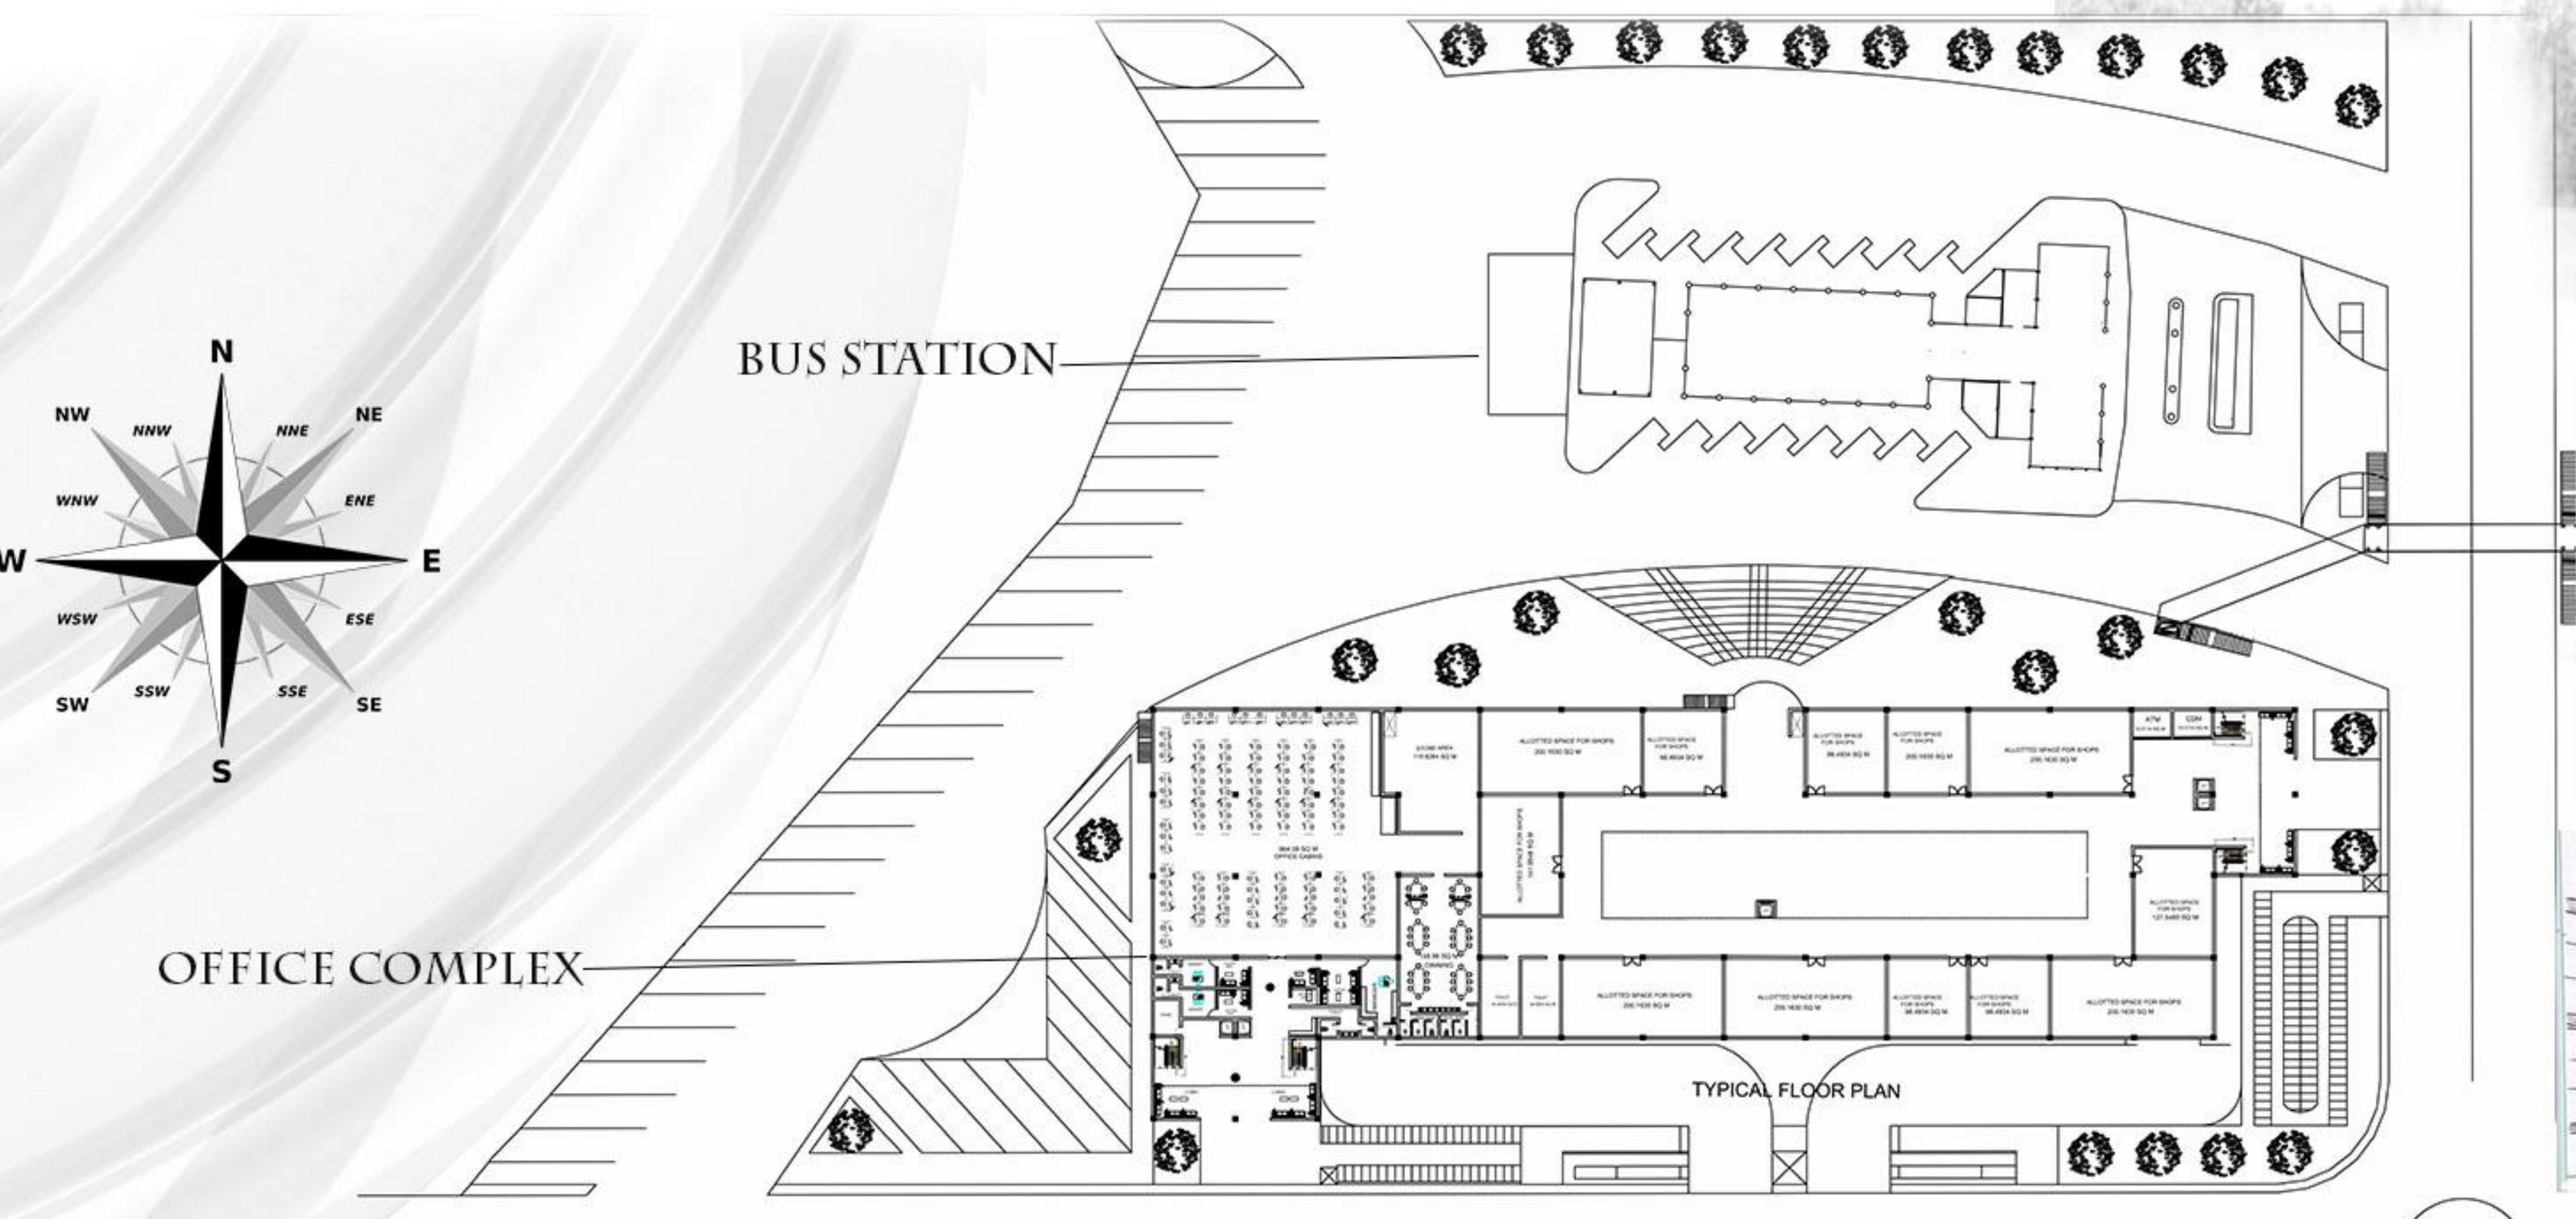

# NASA Sheets

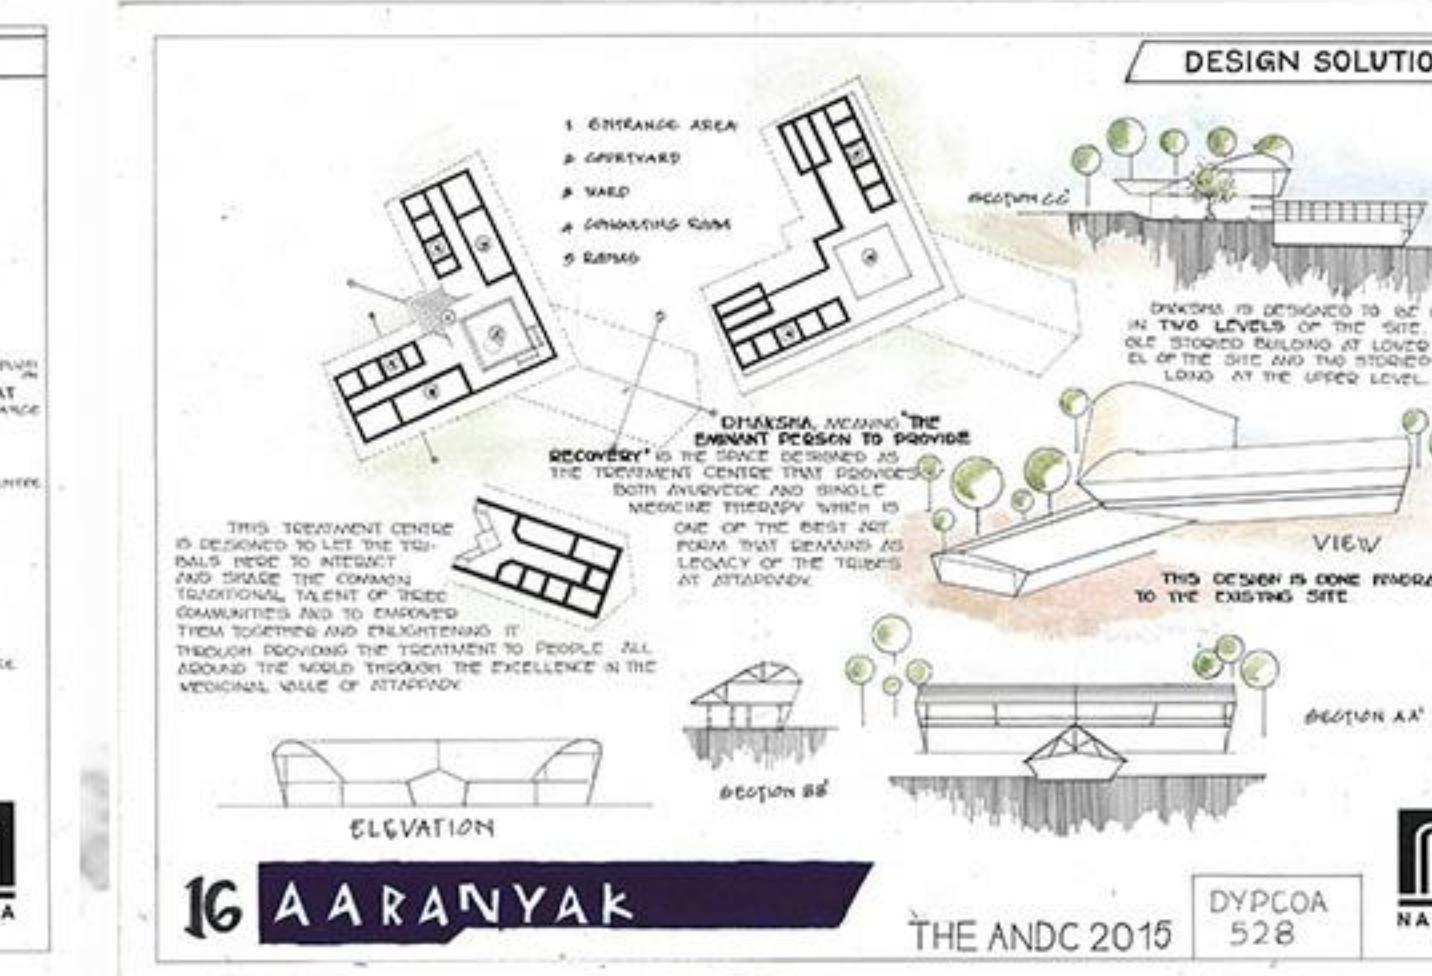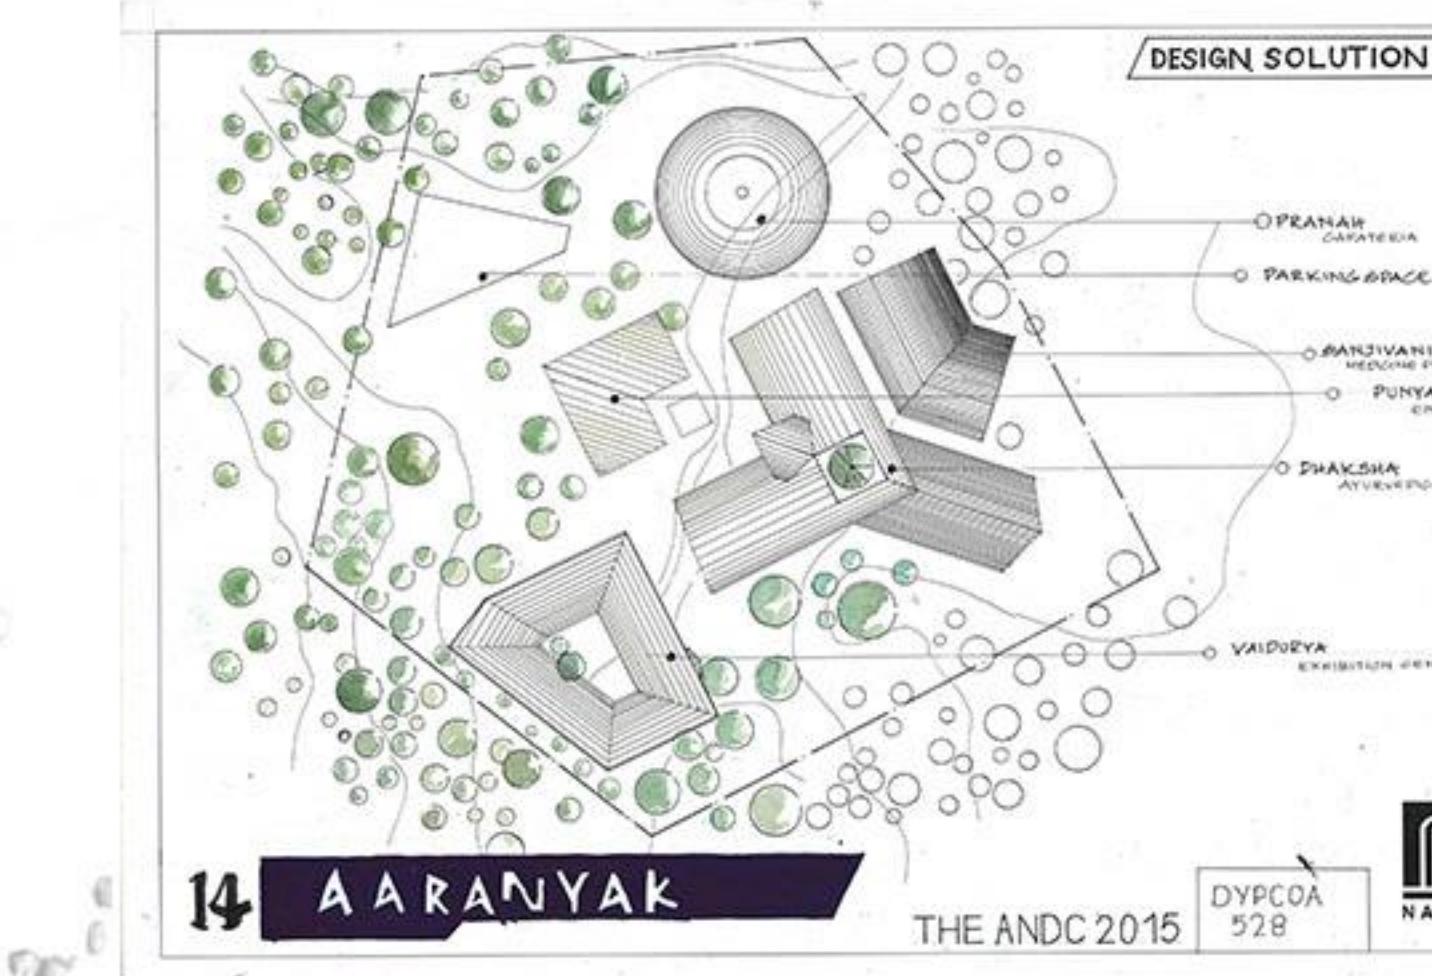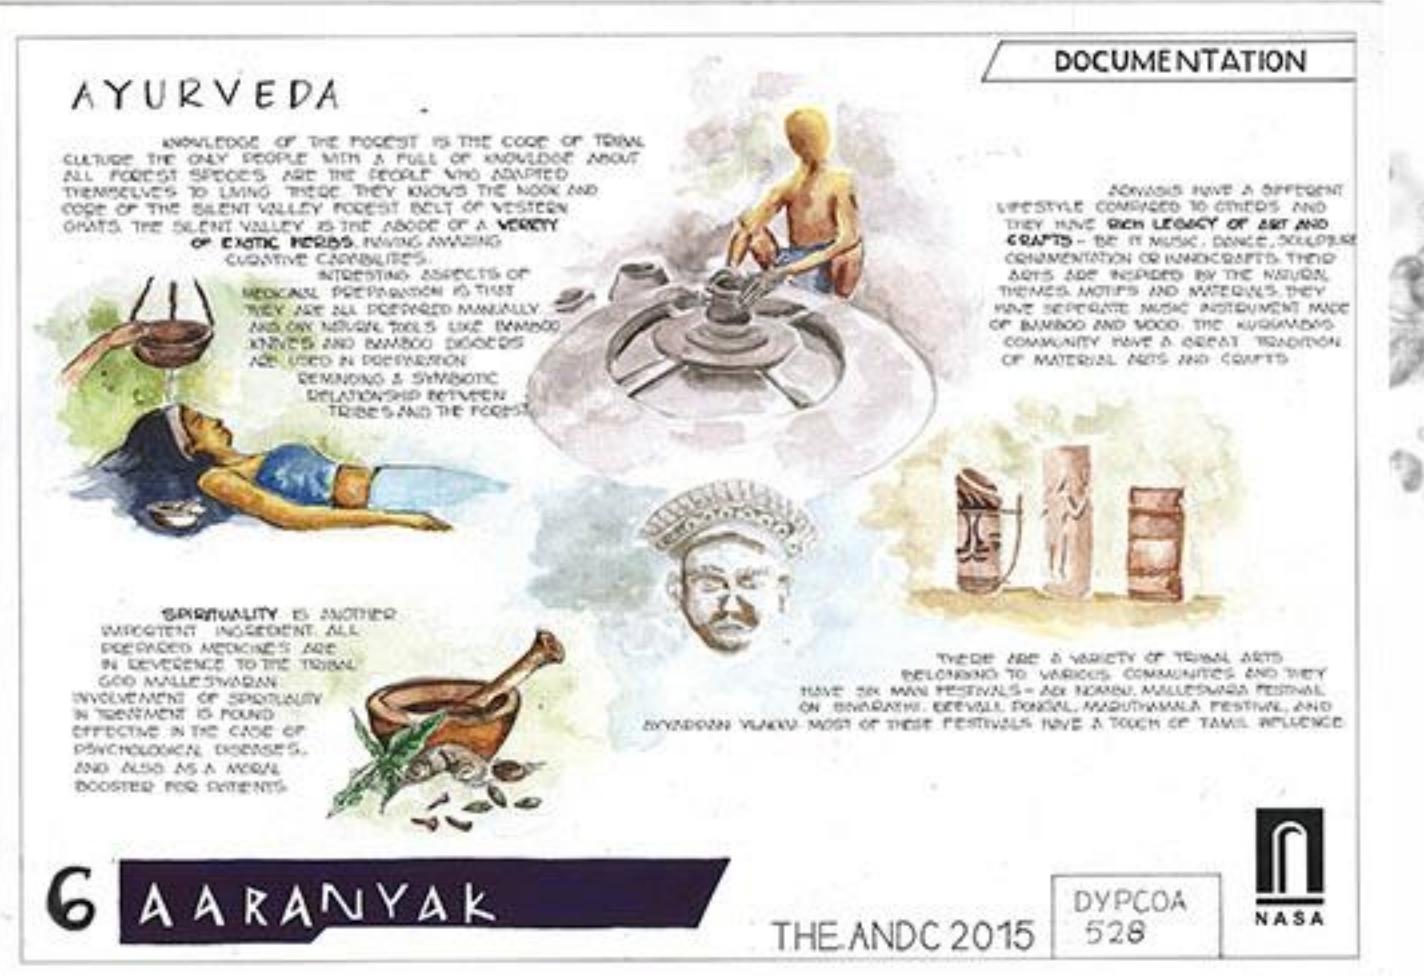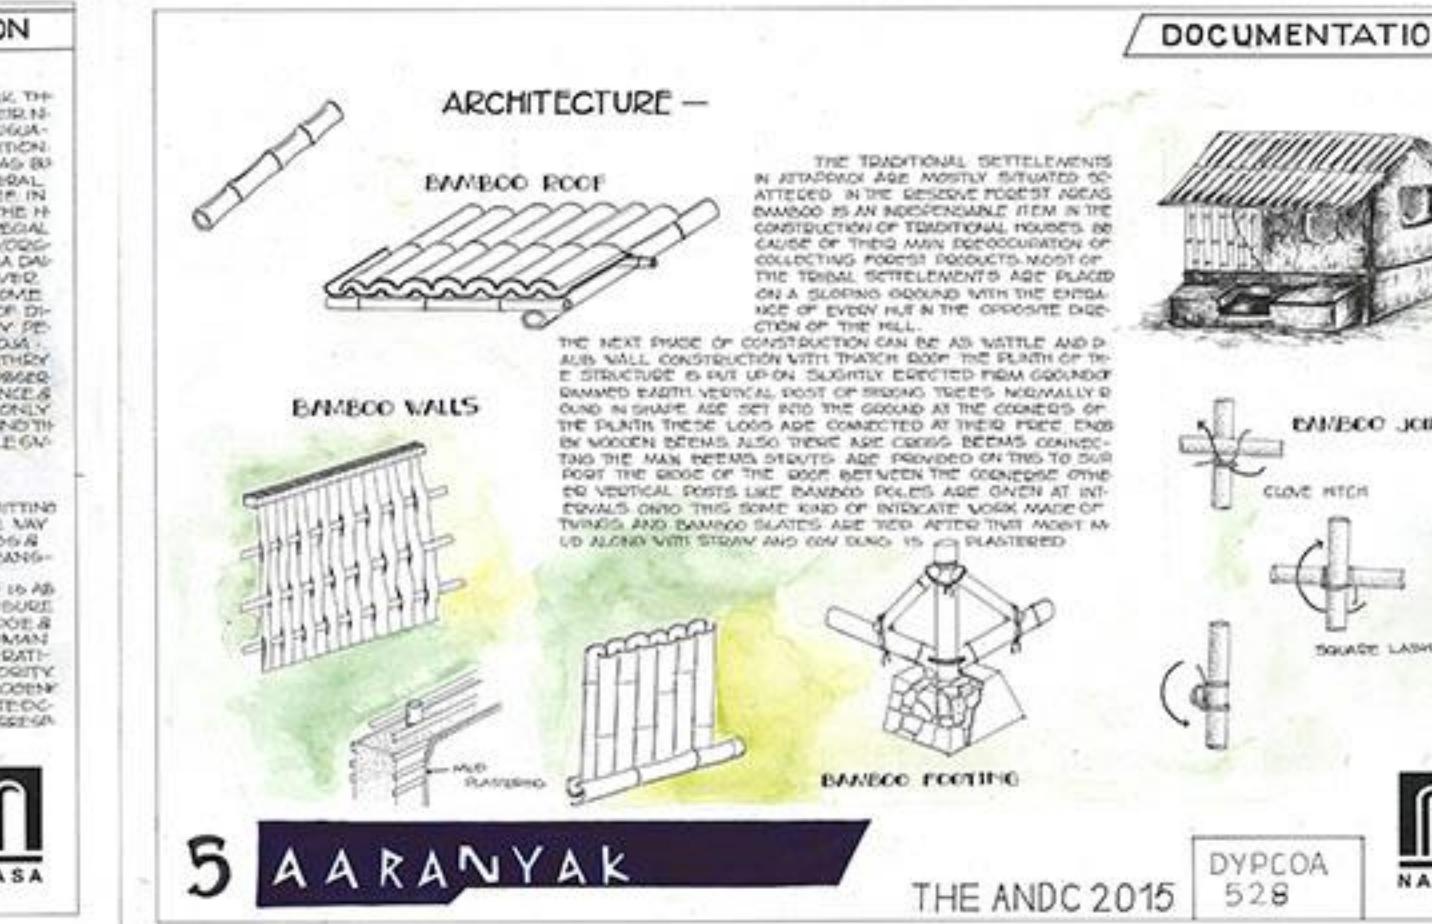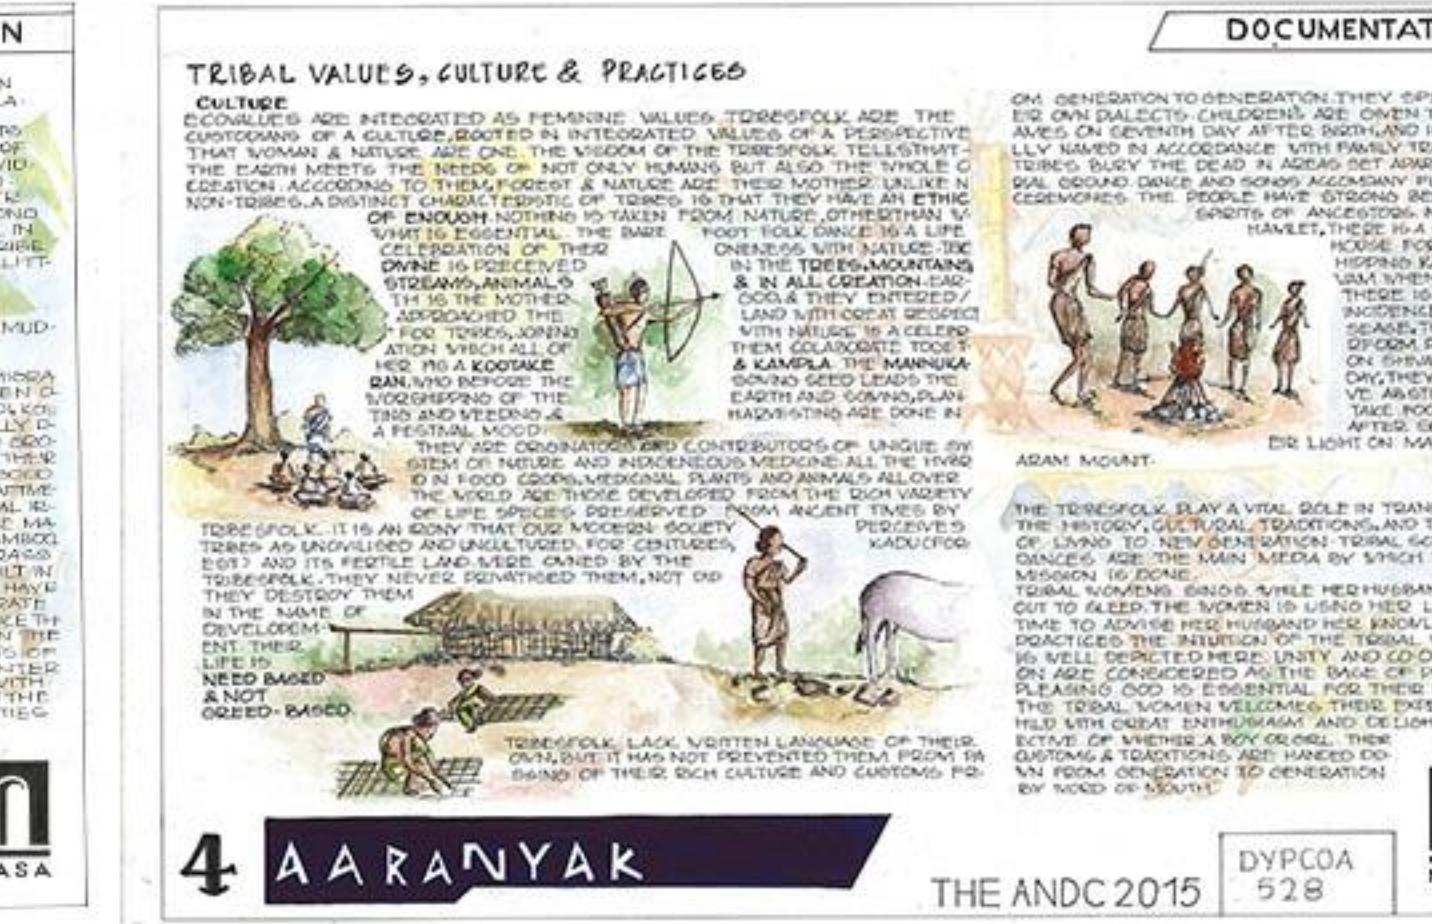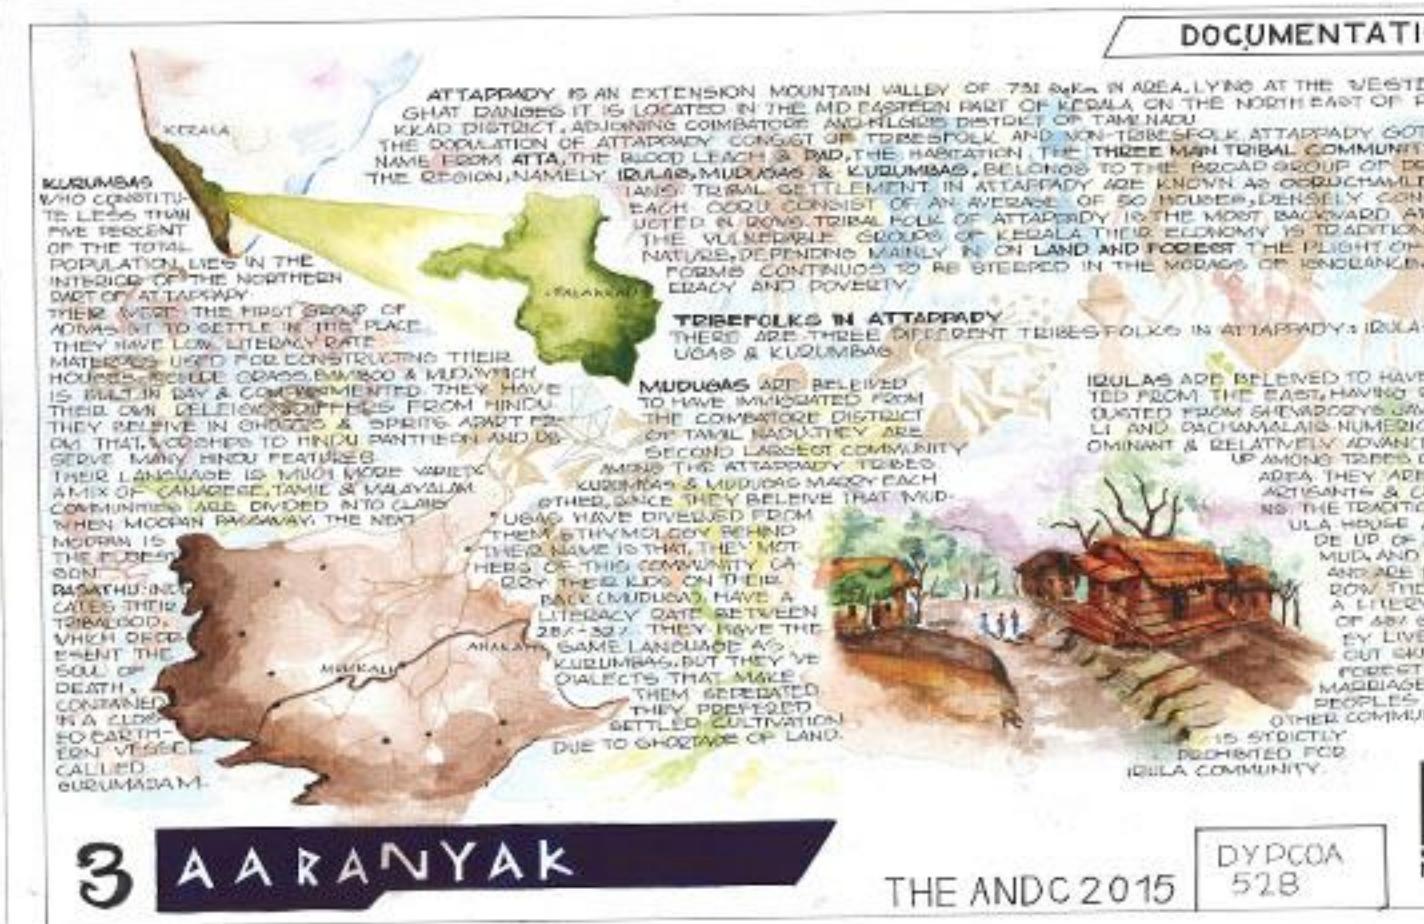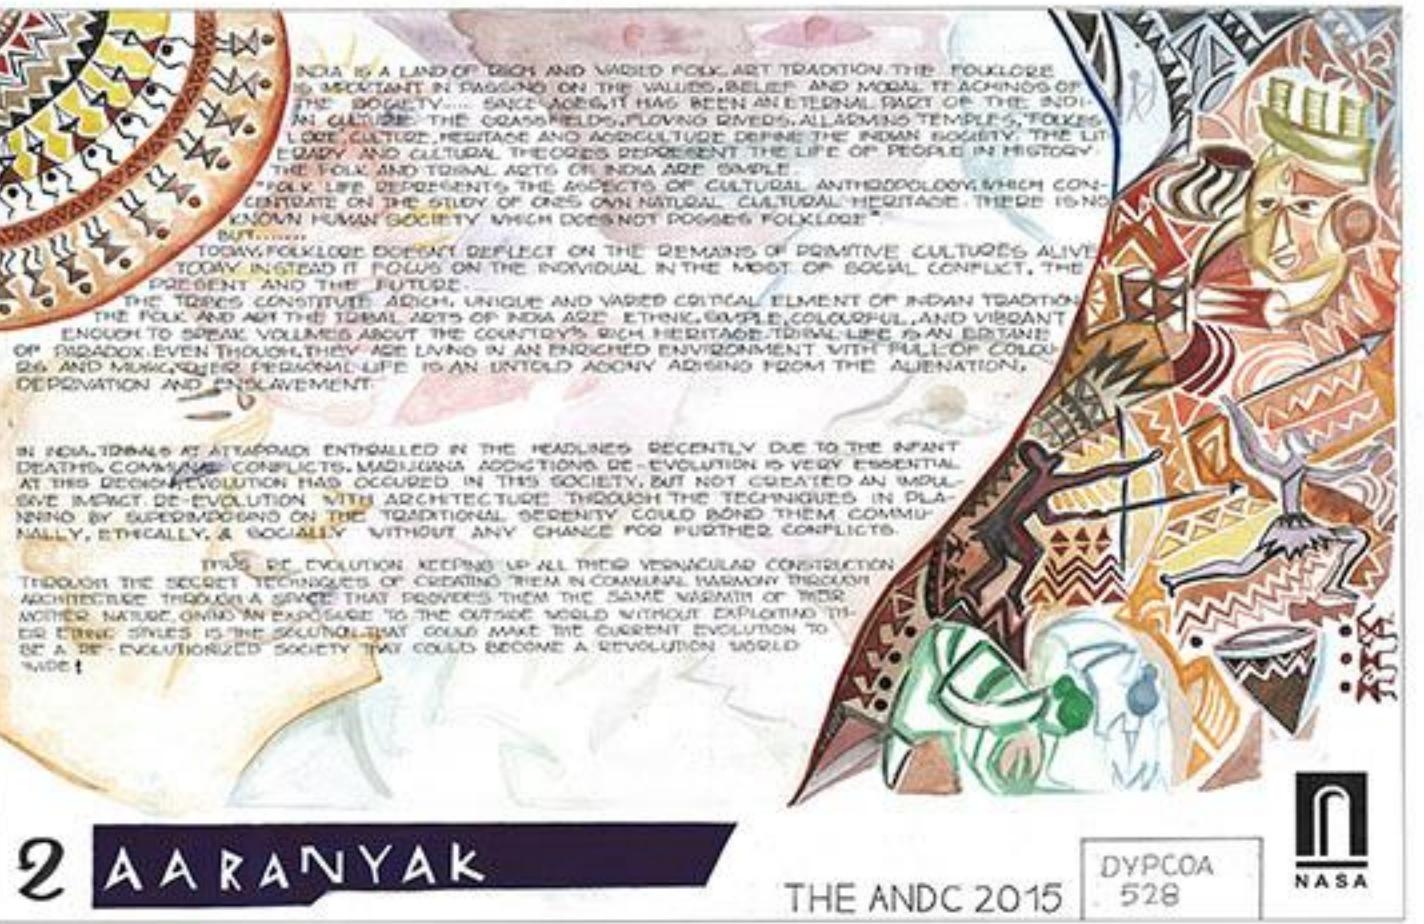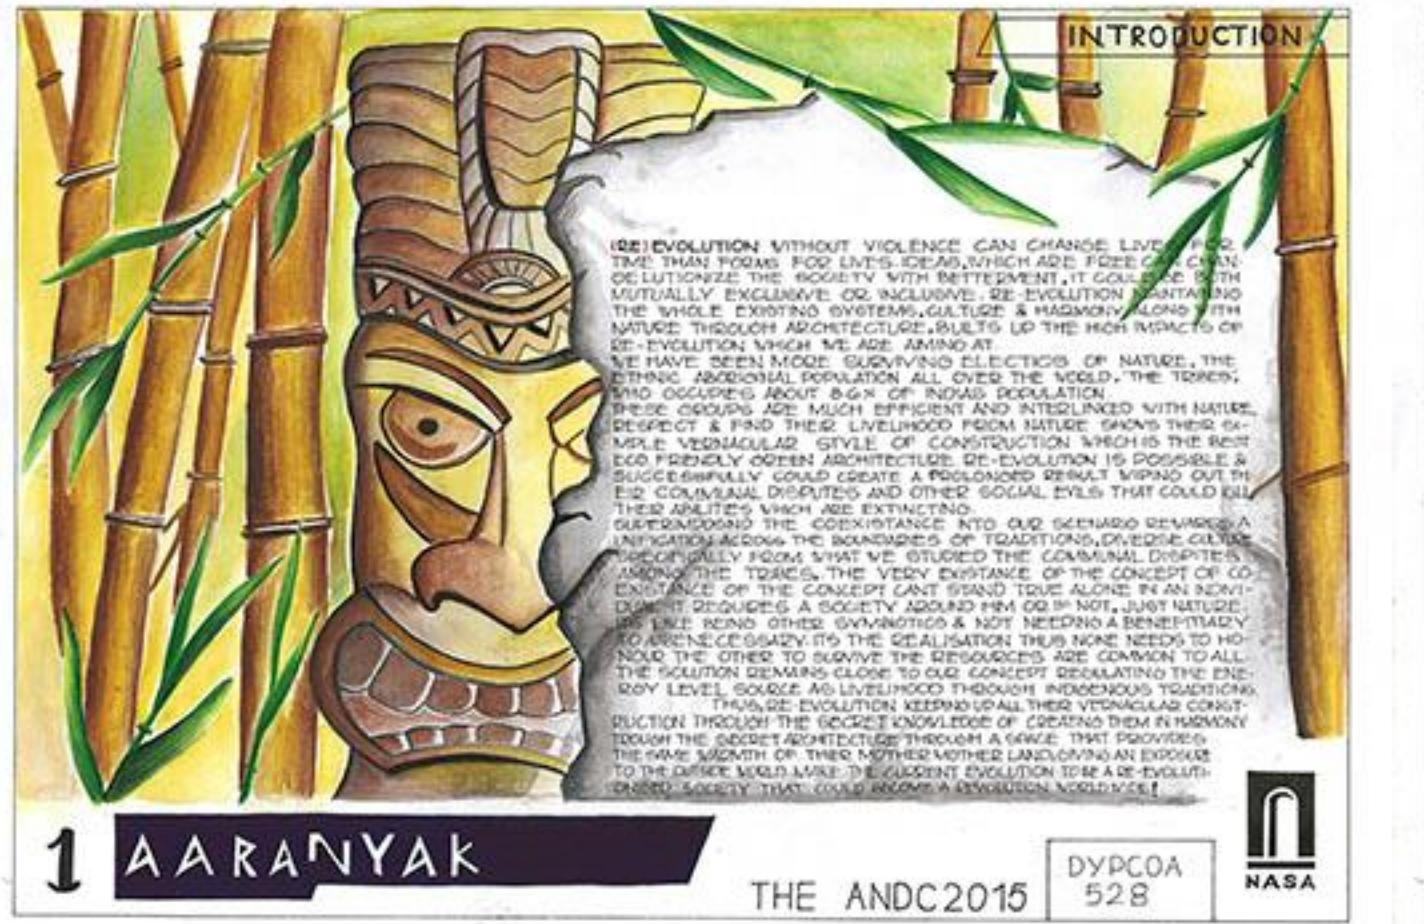

## LOGO DESIGN

## GATEWAY DESIGN


## ACP DESIGN WORKS

# Beyond Class Works

- Logo design for MCC ARTS & sports club.



- Gateway design for polytechnic college  
@vdy

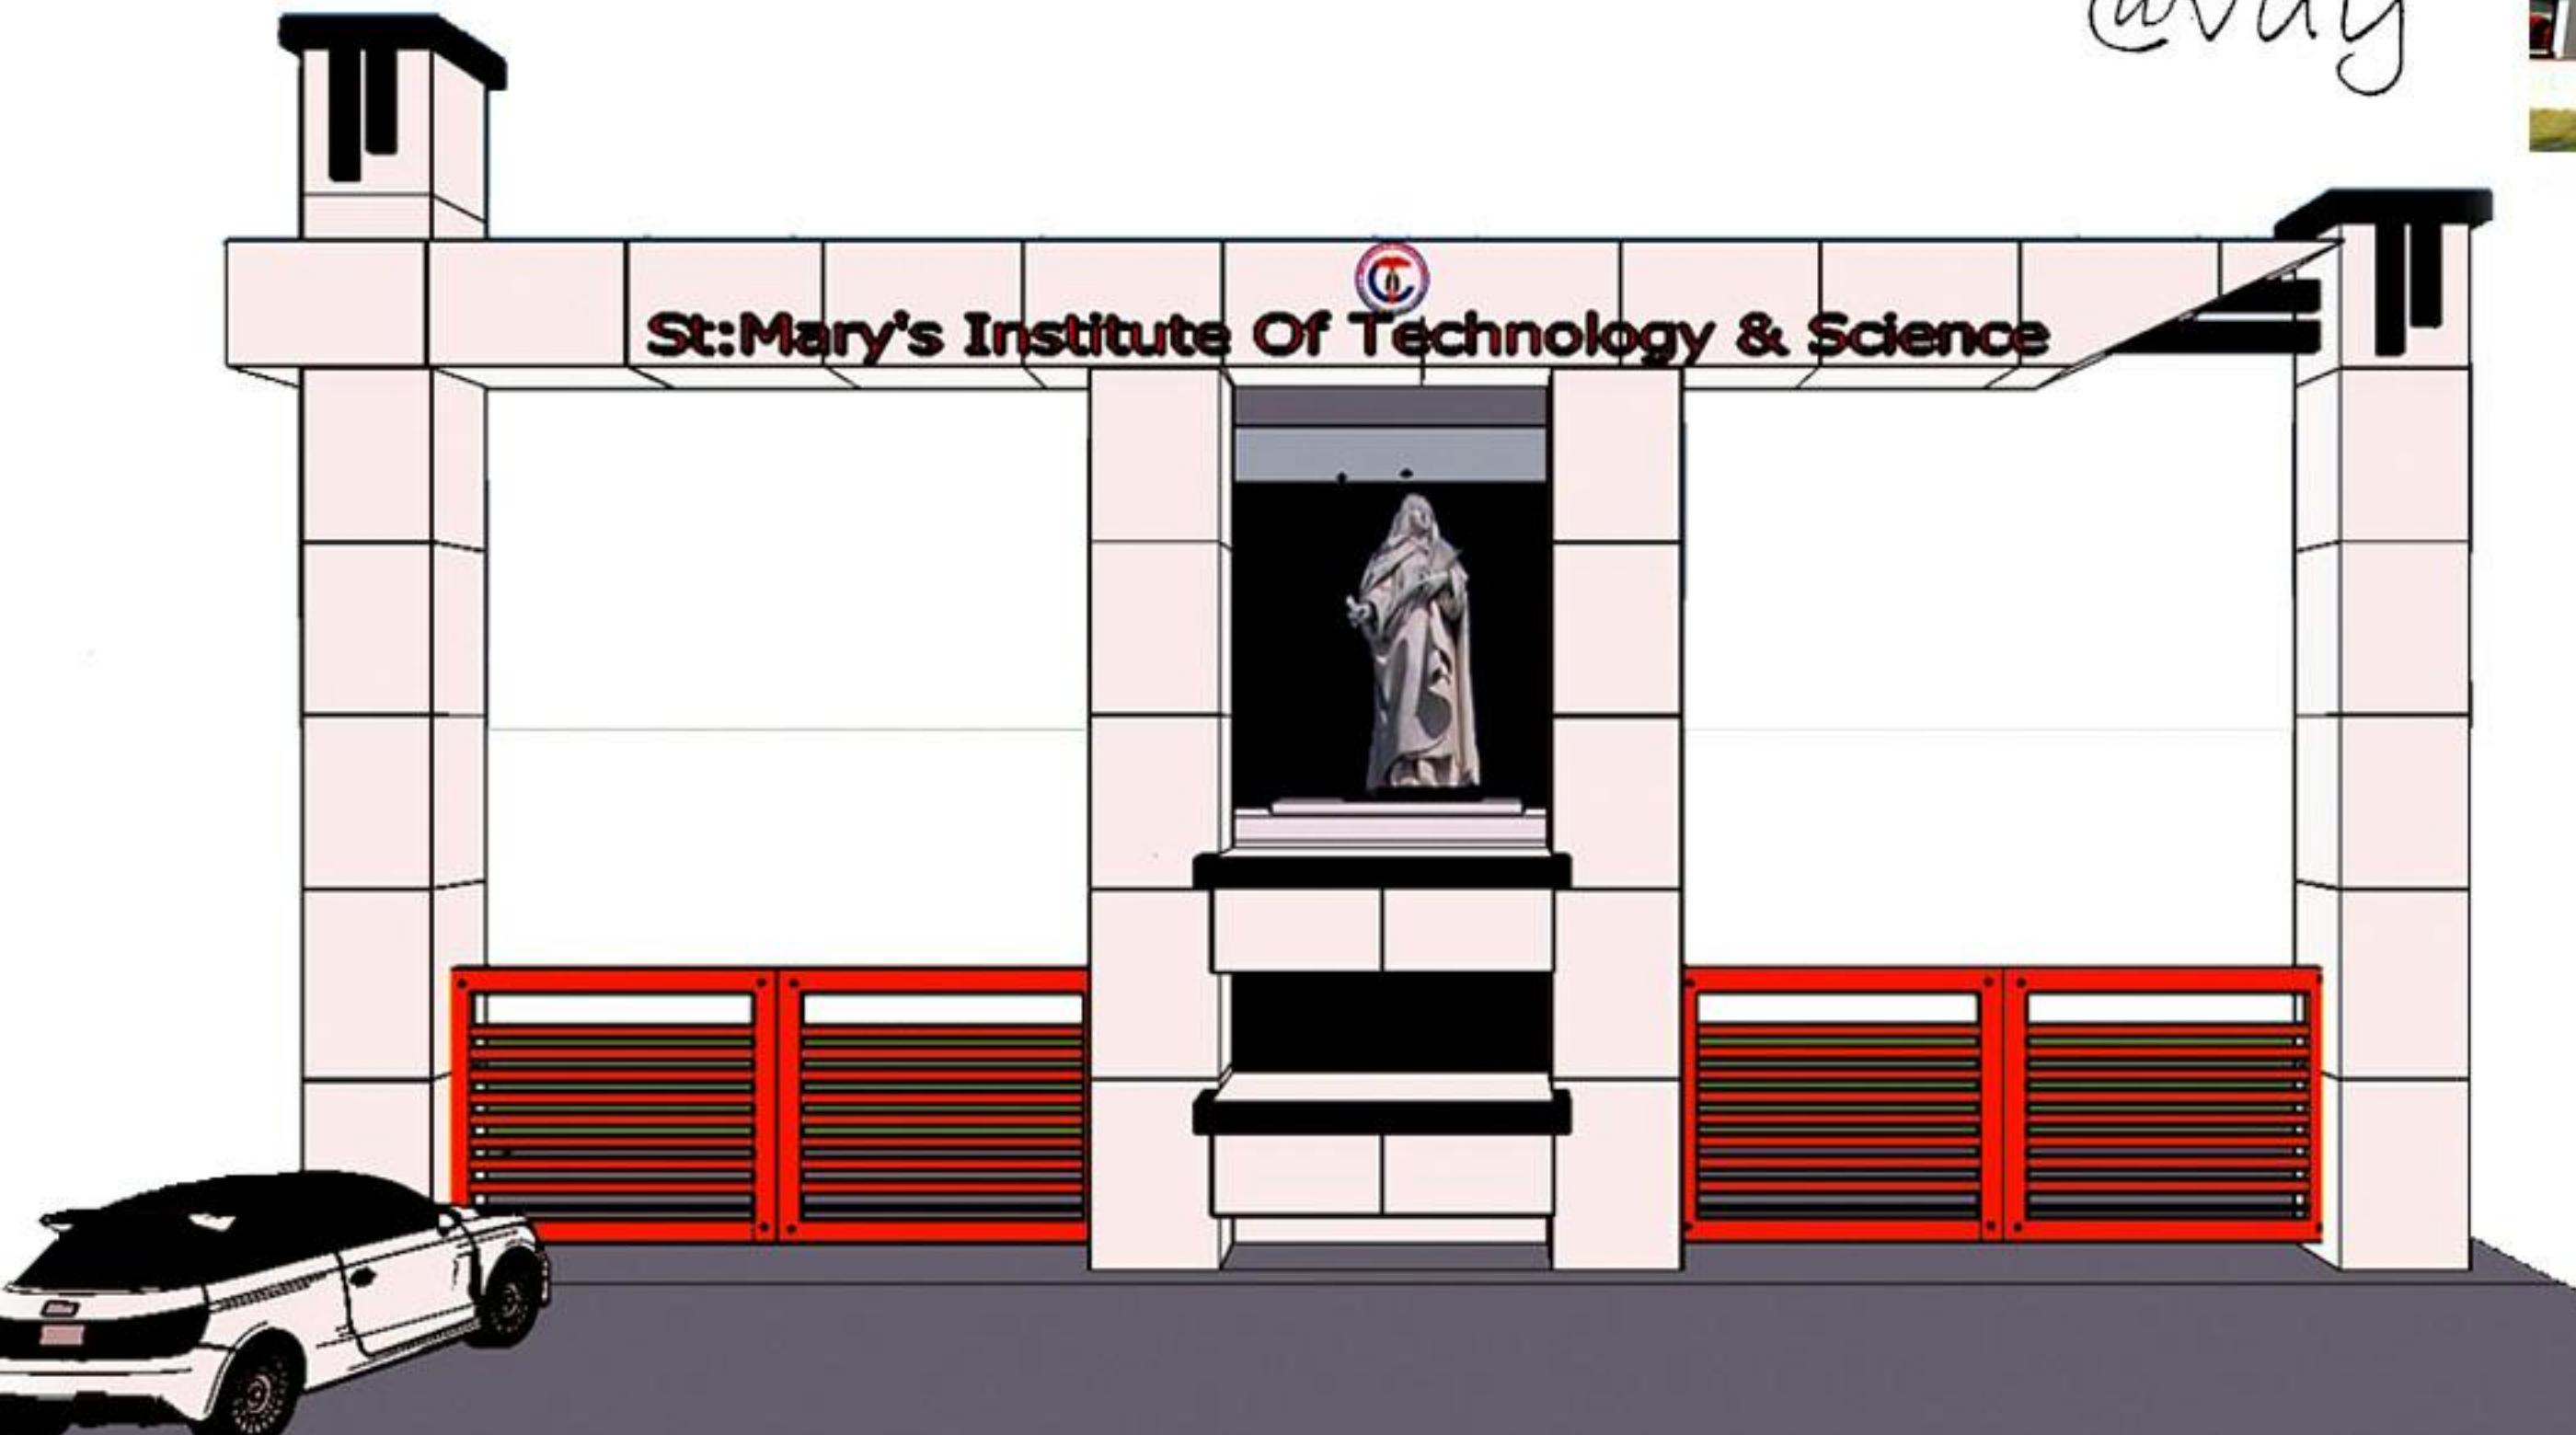

Acp work @ vdy -



my works

# Certificates



*Where there is a will, there is a way. If there is a chance  
in a mission that you can do something, anything, to keep what you  
want from ending, do it. Pry the door open or, if need be, wedge your foot  
in that door and keep it open.*

العربية